


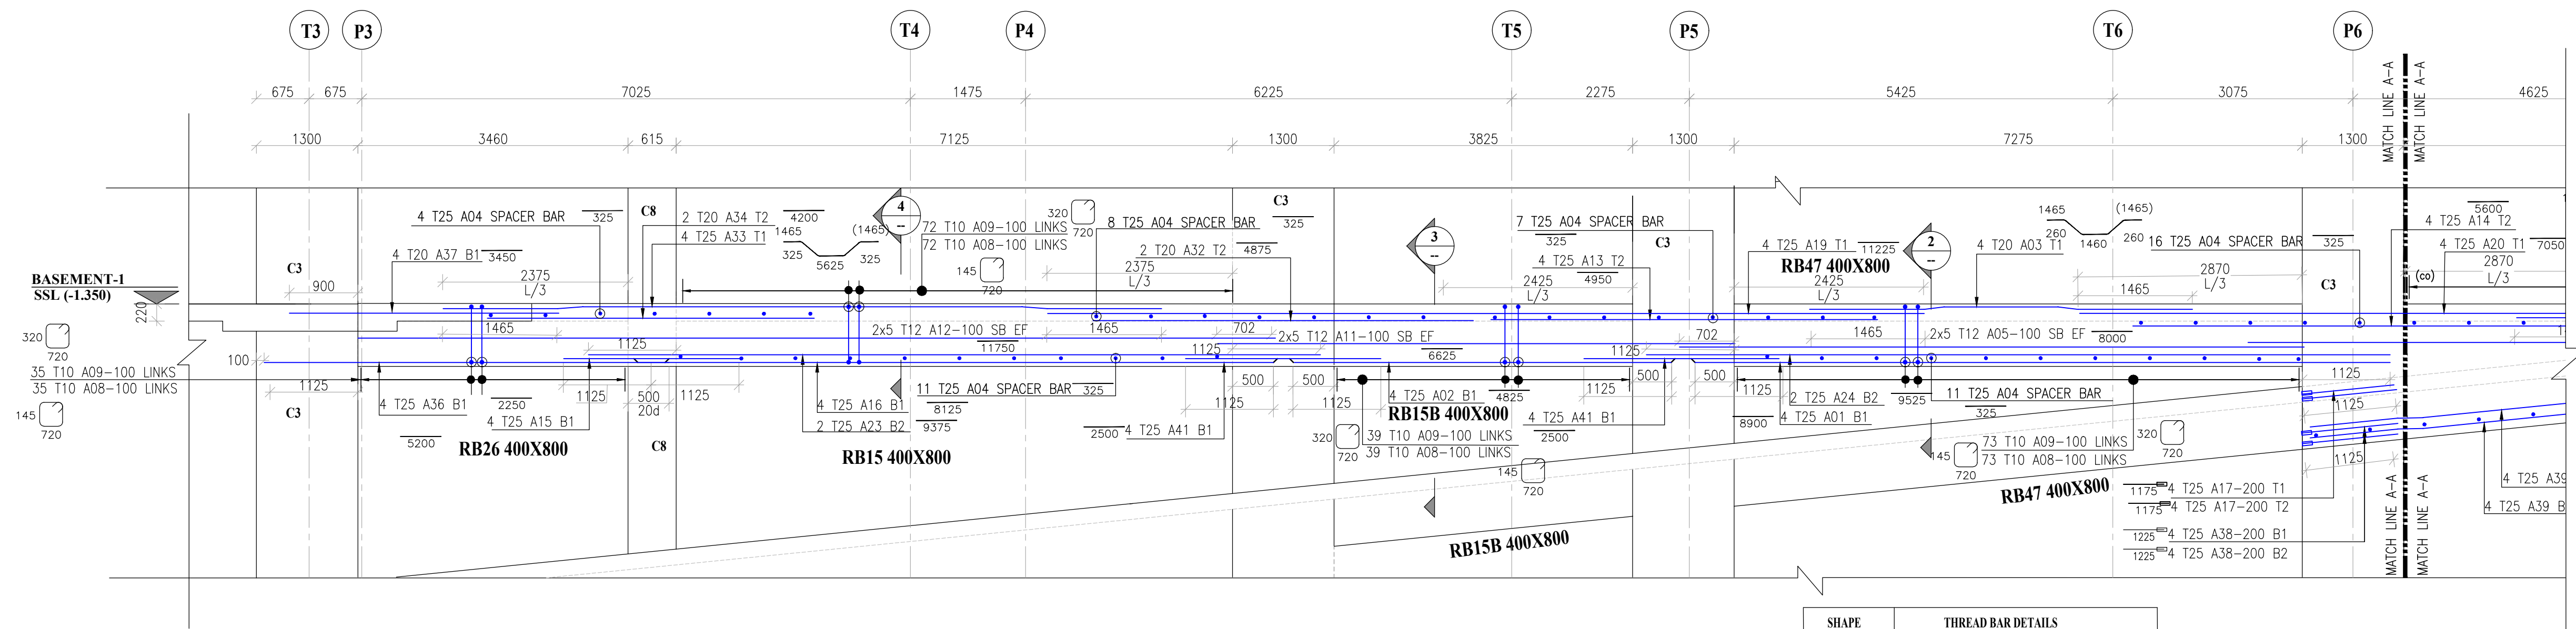


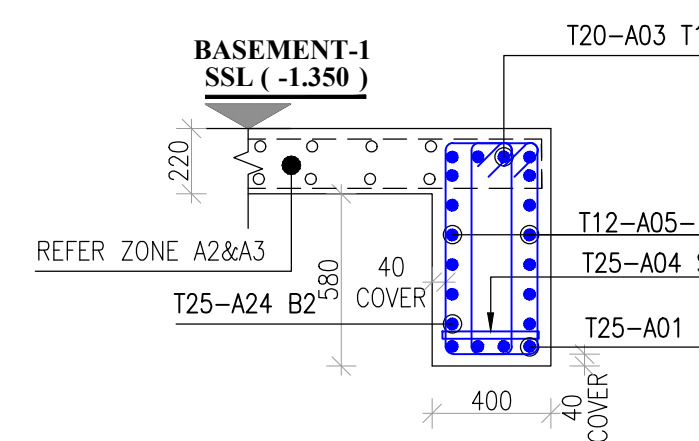


SHAPE	THREAD BAR DETAILS
990001 A	(ONE SIDE HALF THREADED + COUPLER)
990012 A	(ONE SIDE HALF THREADED ONLY)
B A 990003	(C SIDE HALF THREADED ONLY)

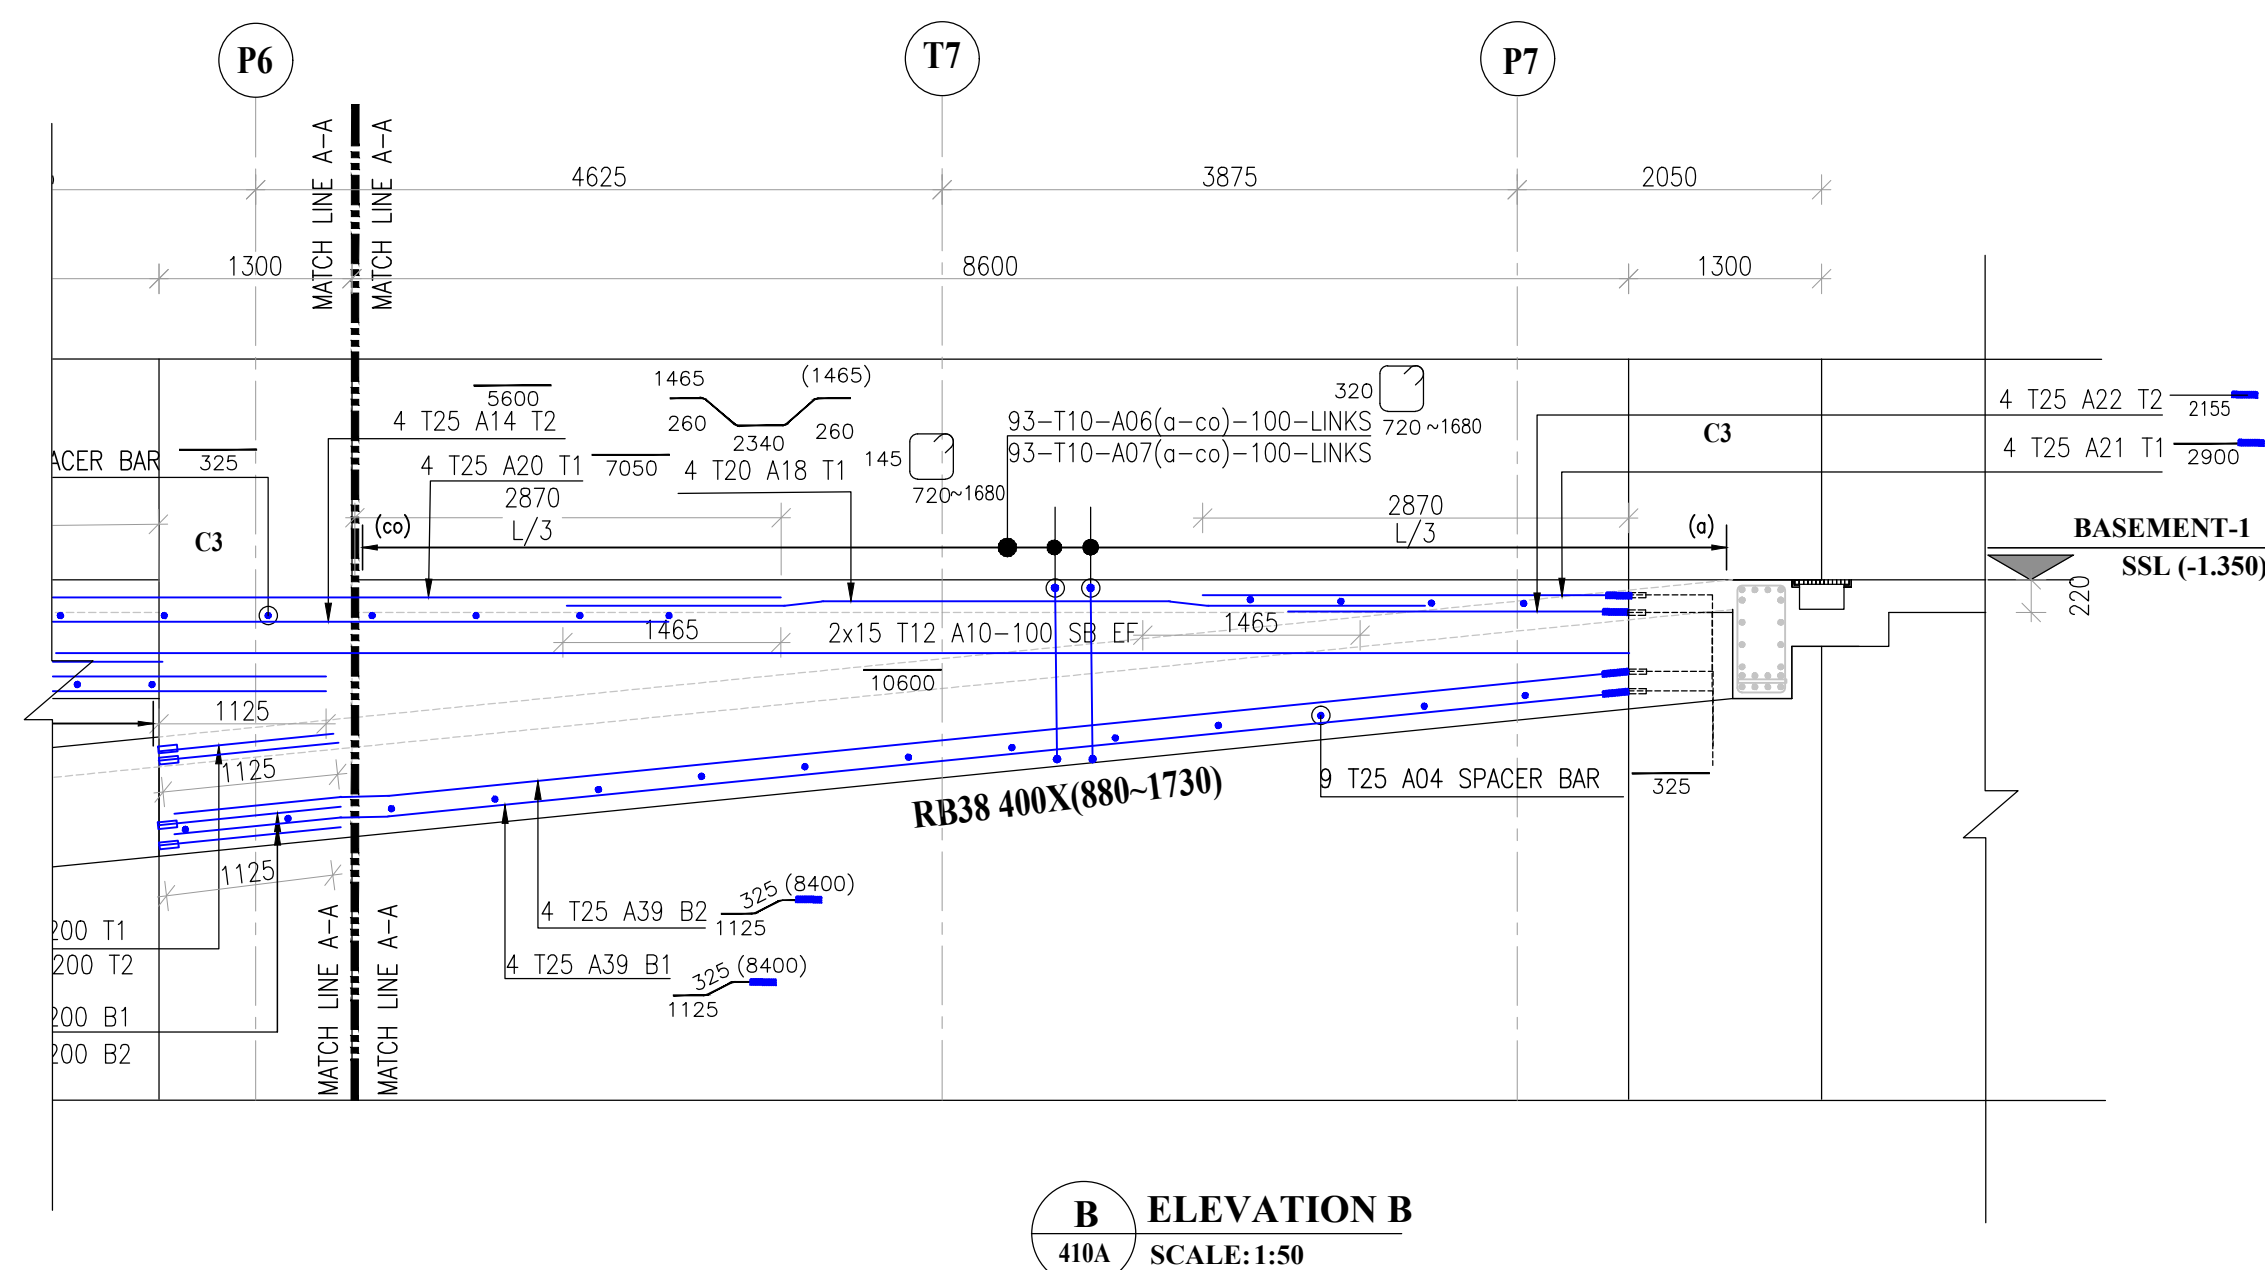

LINK DETAILS-02

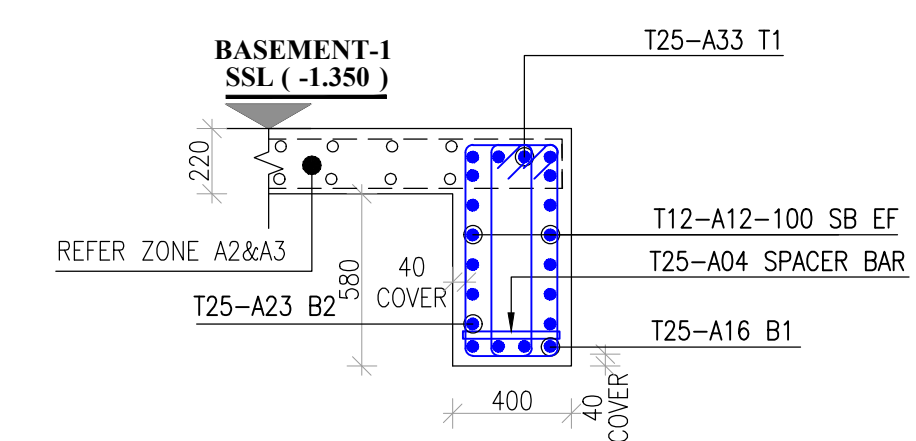

LINK DETAILS-04

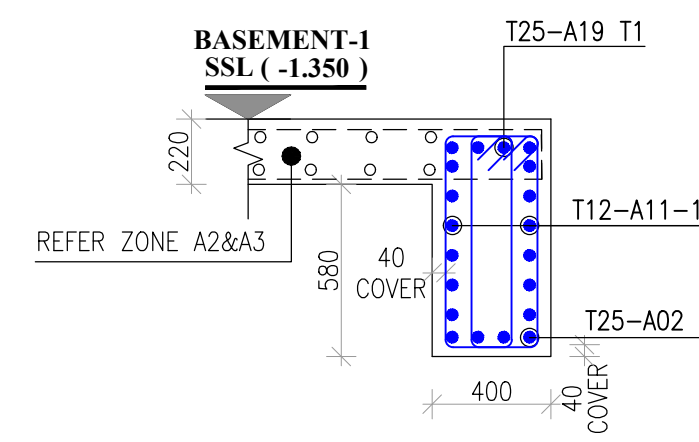

LINK DETAILS-03

PLOT-4 RAMP BEAMS REINFORCEMENT DETAILS

SCALE 1:50