



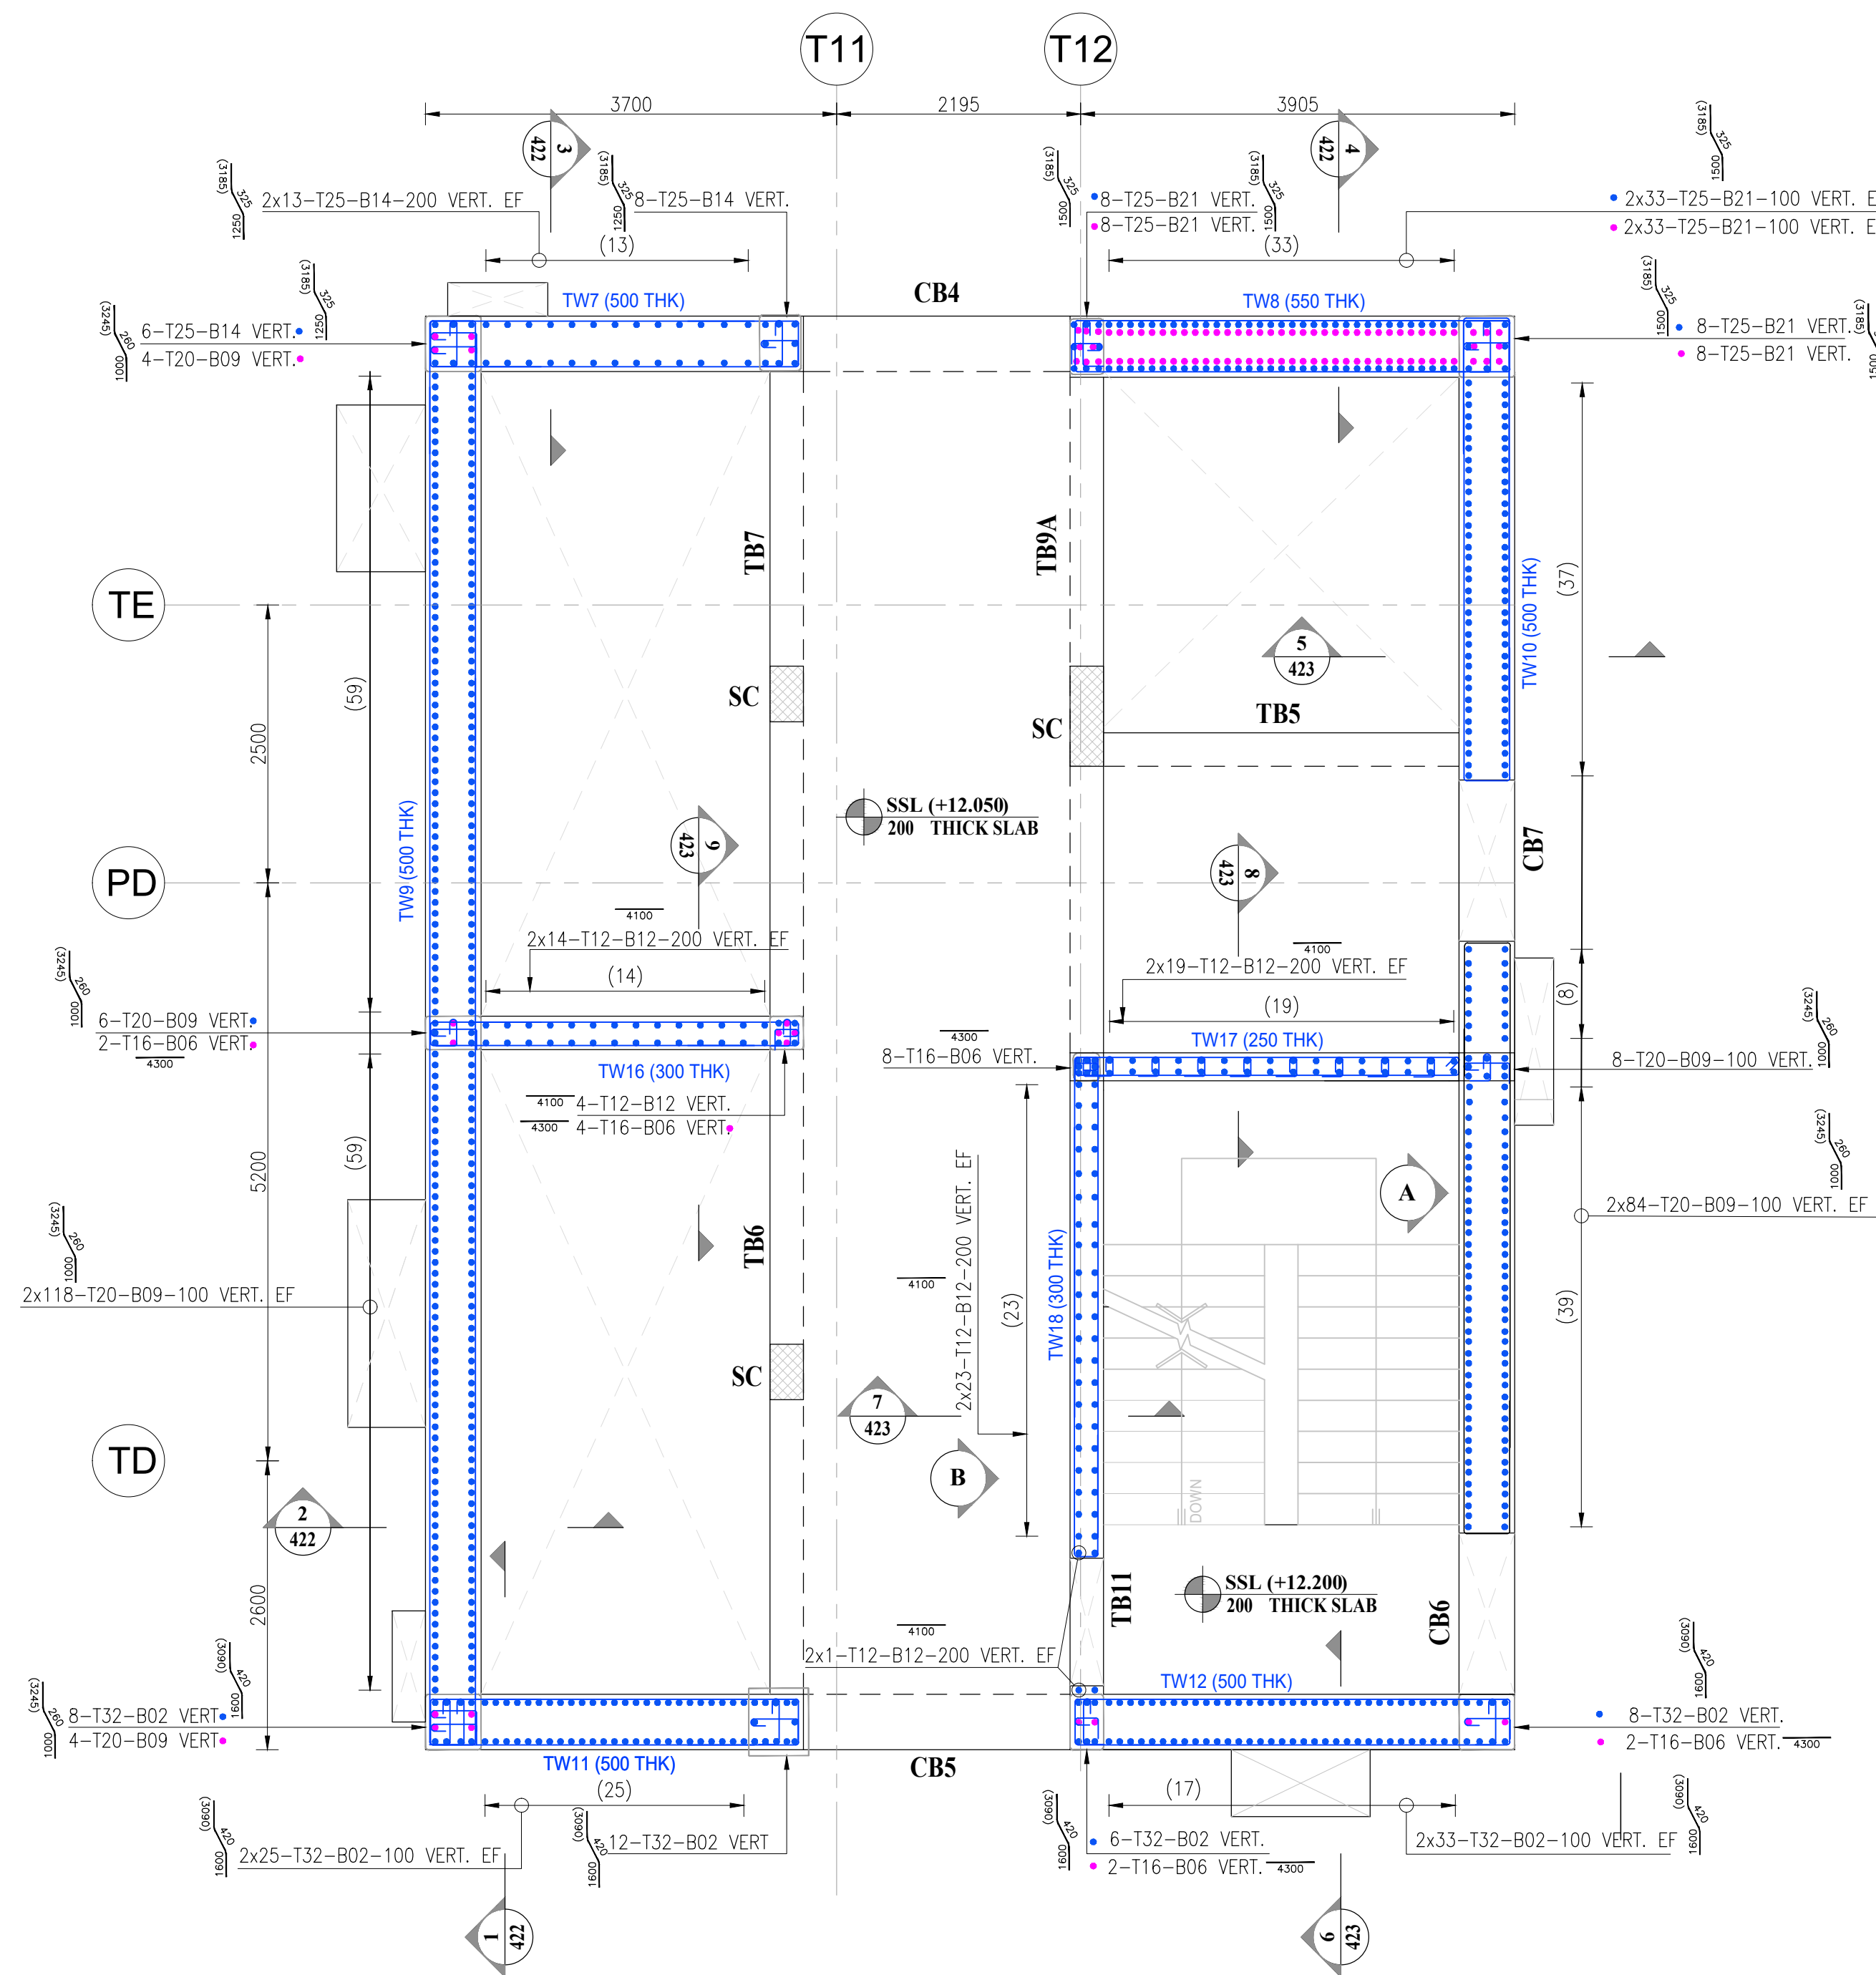

DETAIL-A
TOWER CORE WALL VERTICAL REINFORCEMENT DETAILS

SCALE 1:50
FROM SECOND FLOOR TO THIRD FLOOR

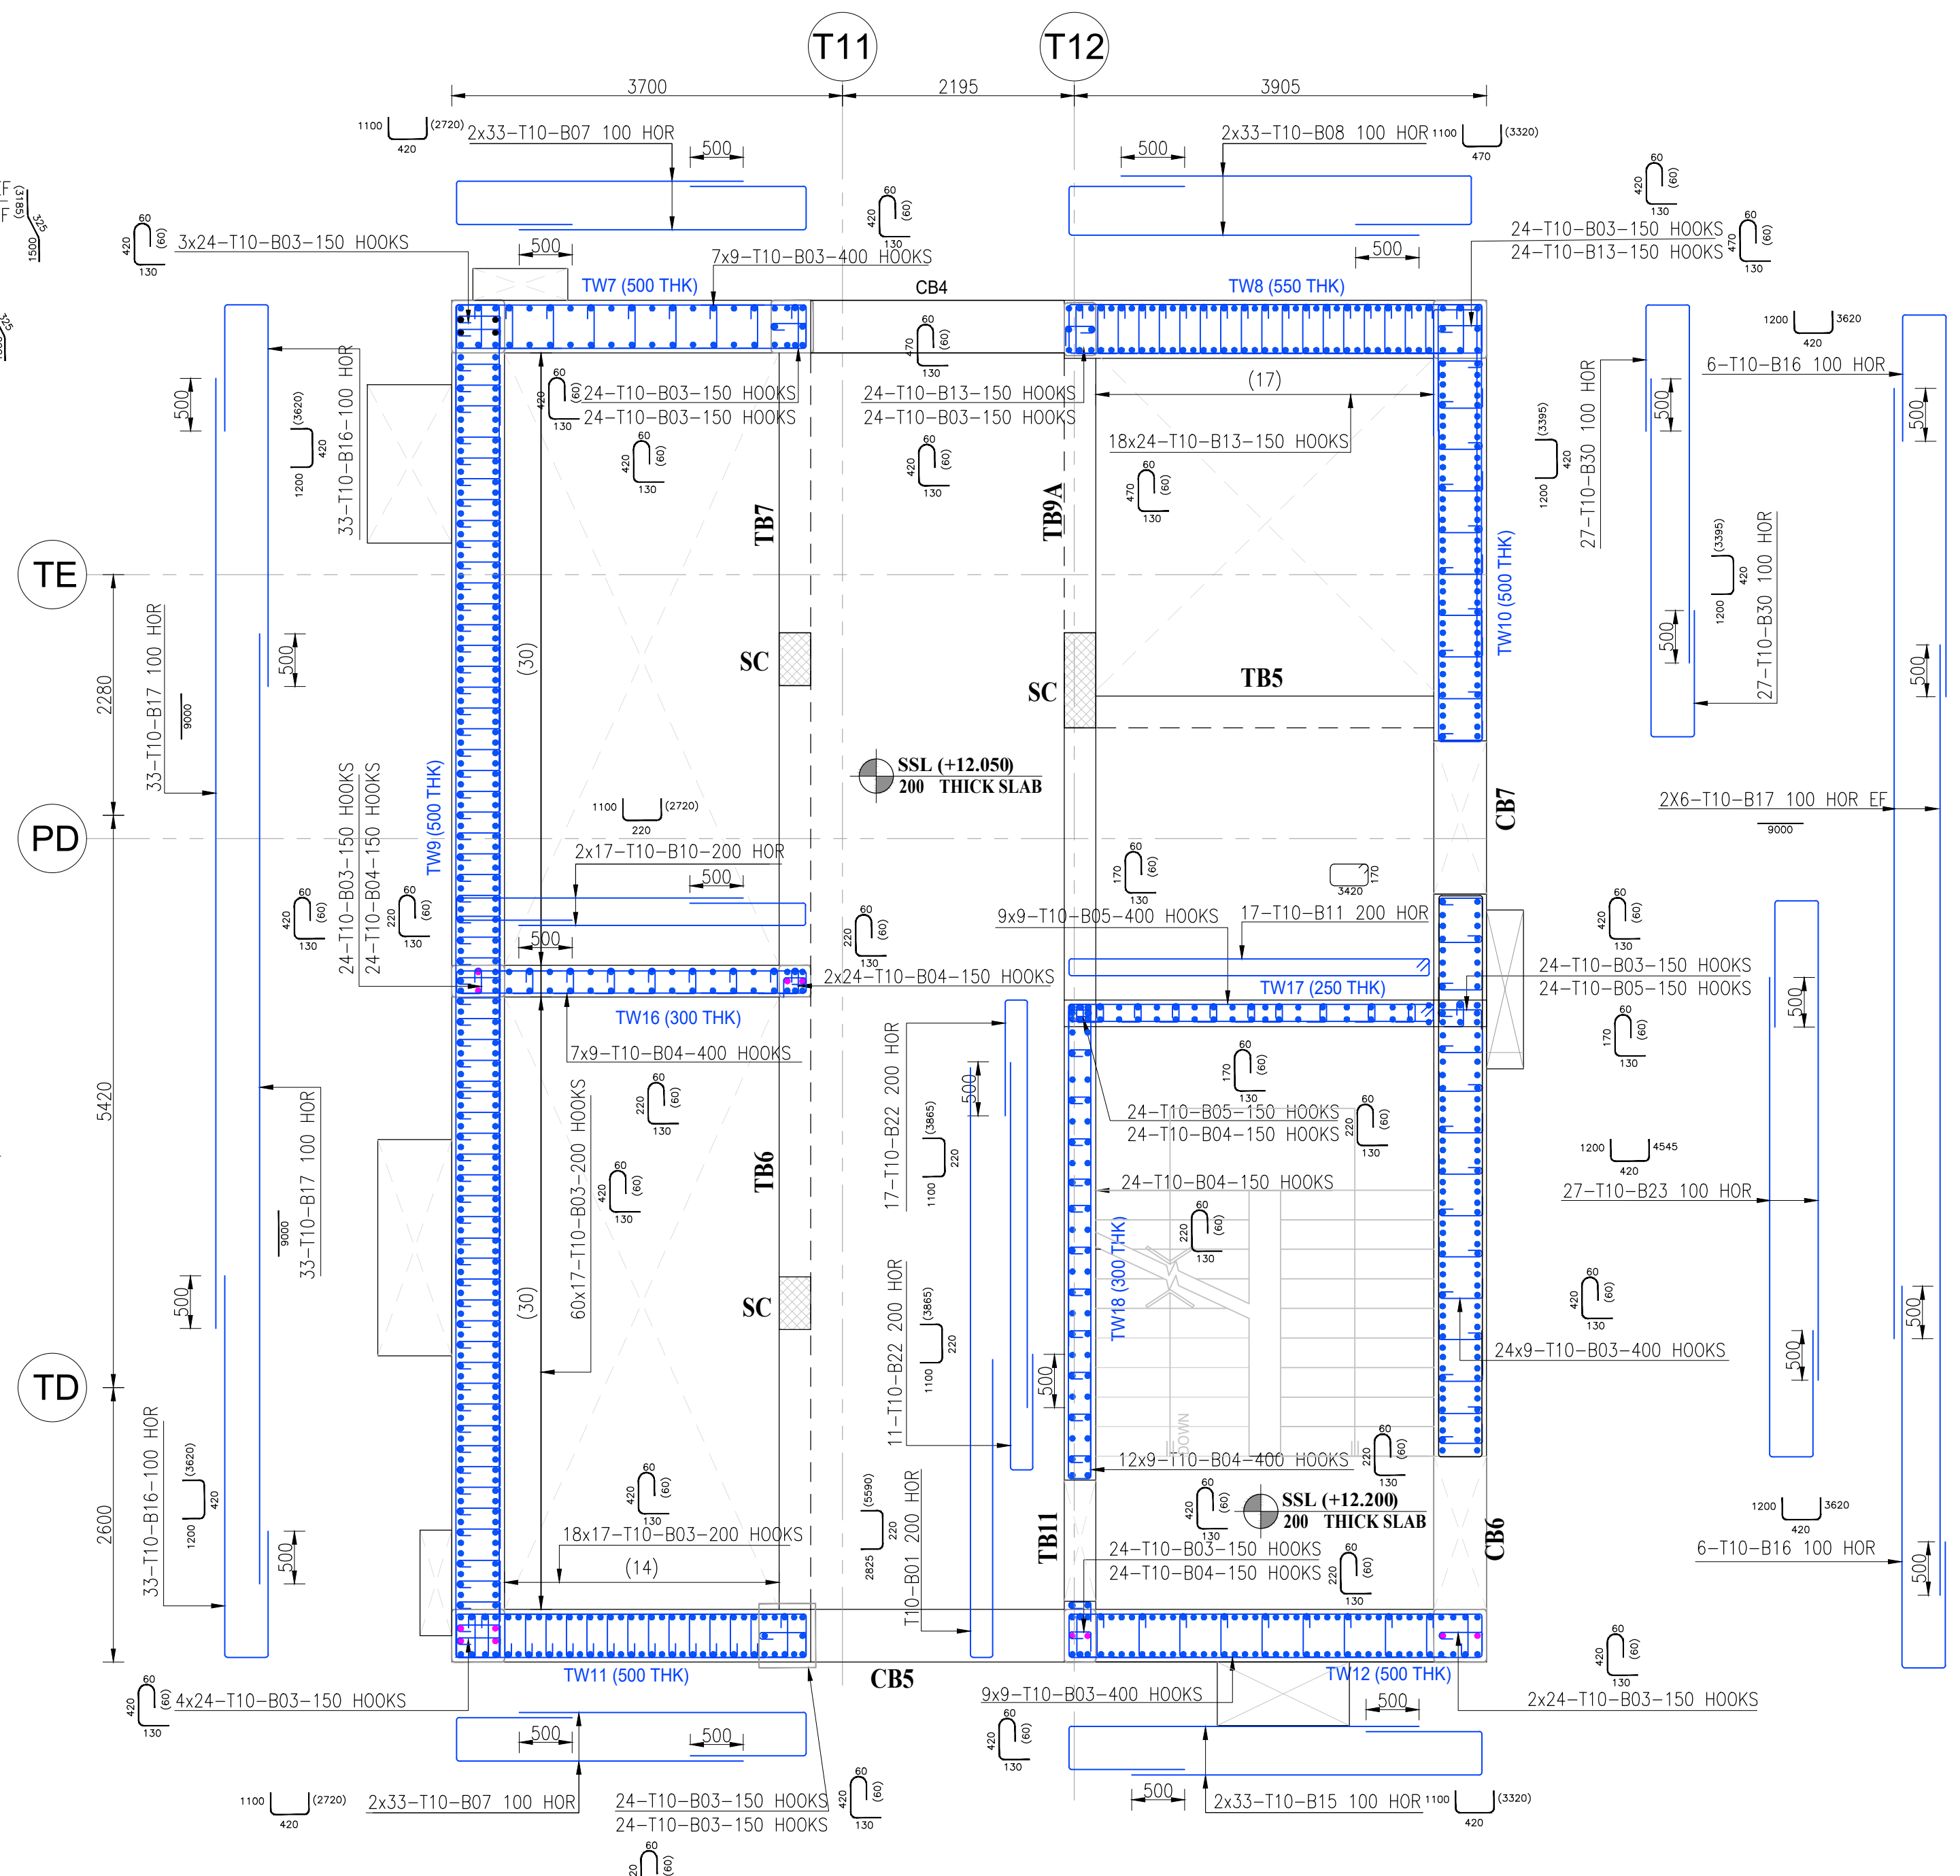

DETAIL-A
TOWER CORE WALL HORIZONTAL REINFORCEMENT DETAILS

SCALE 1:50
FROM SECOND FLOOR TO THIRD FLOOR



KEY PLAN