




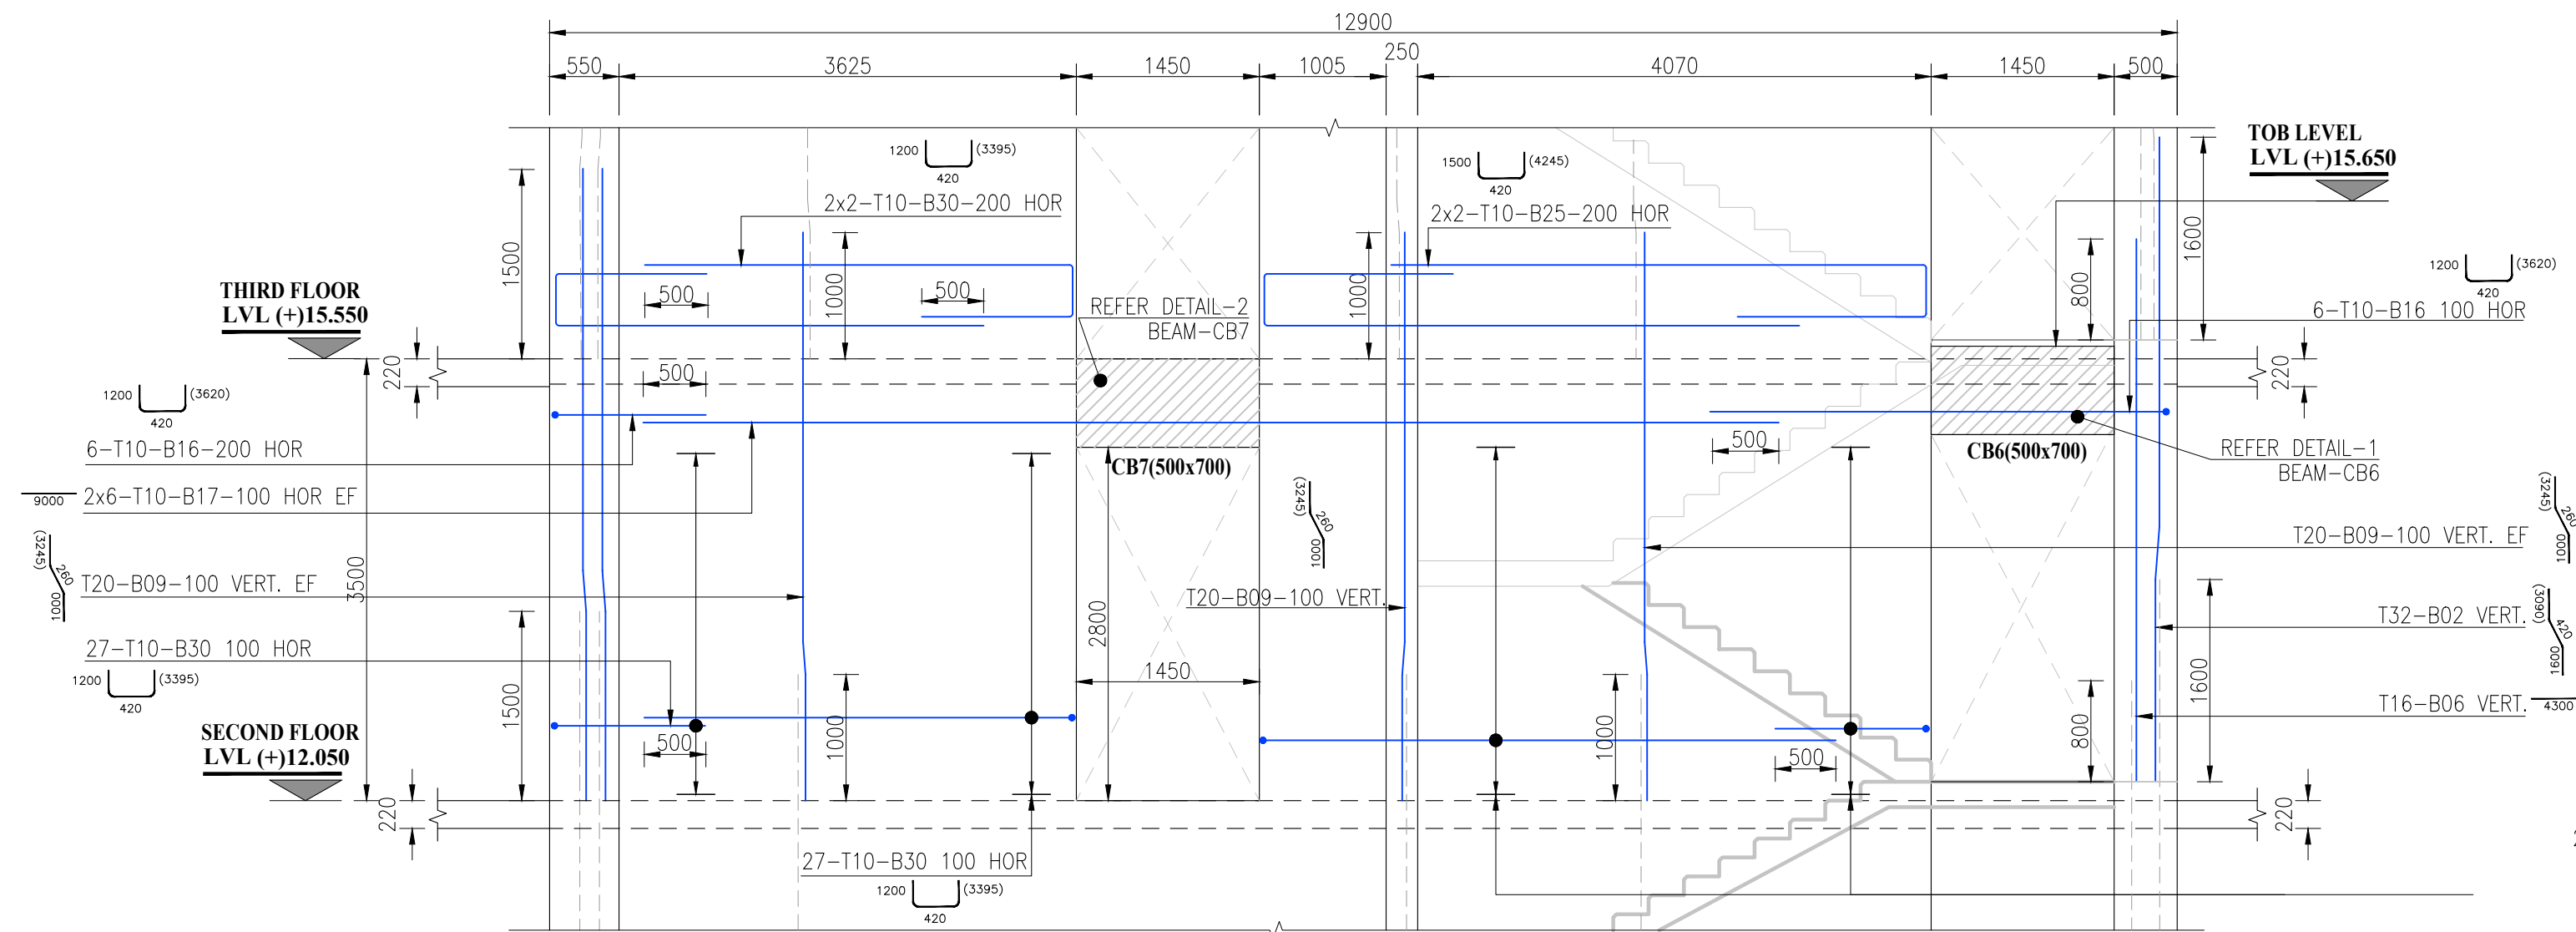


ELEVATION-A
SCALE: 1:50

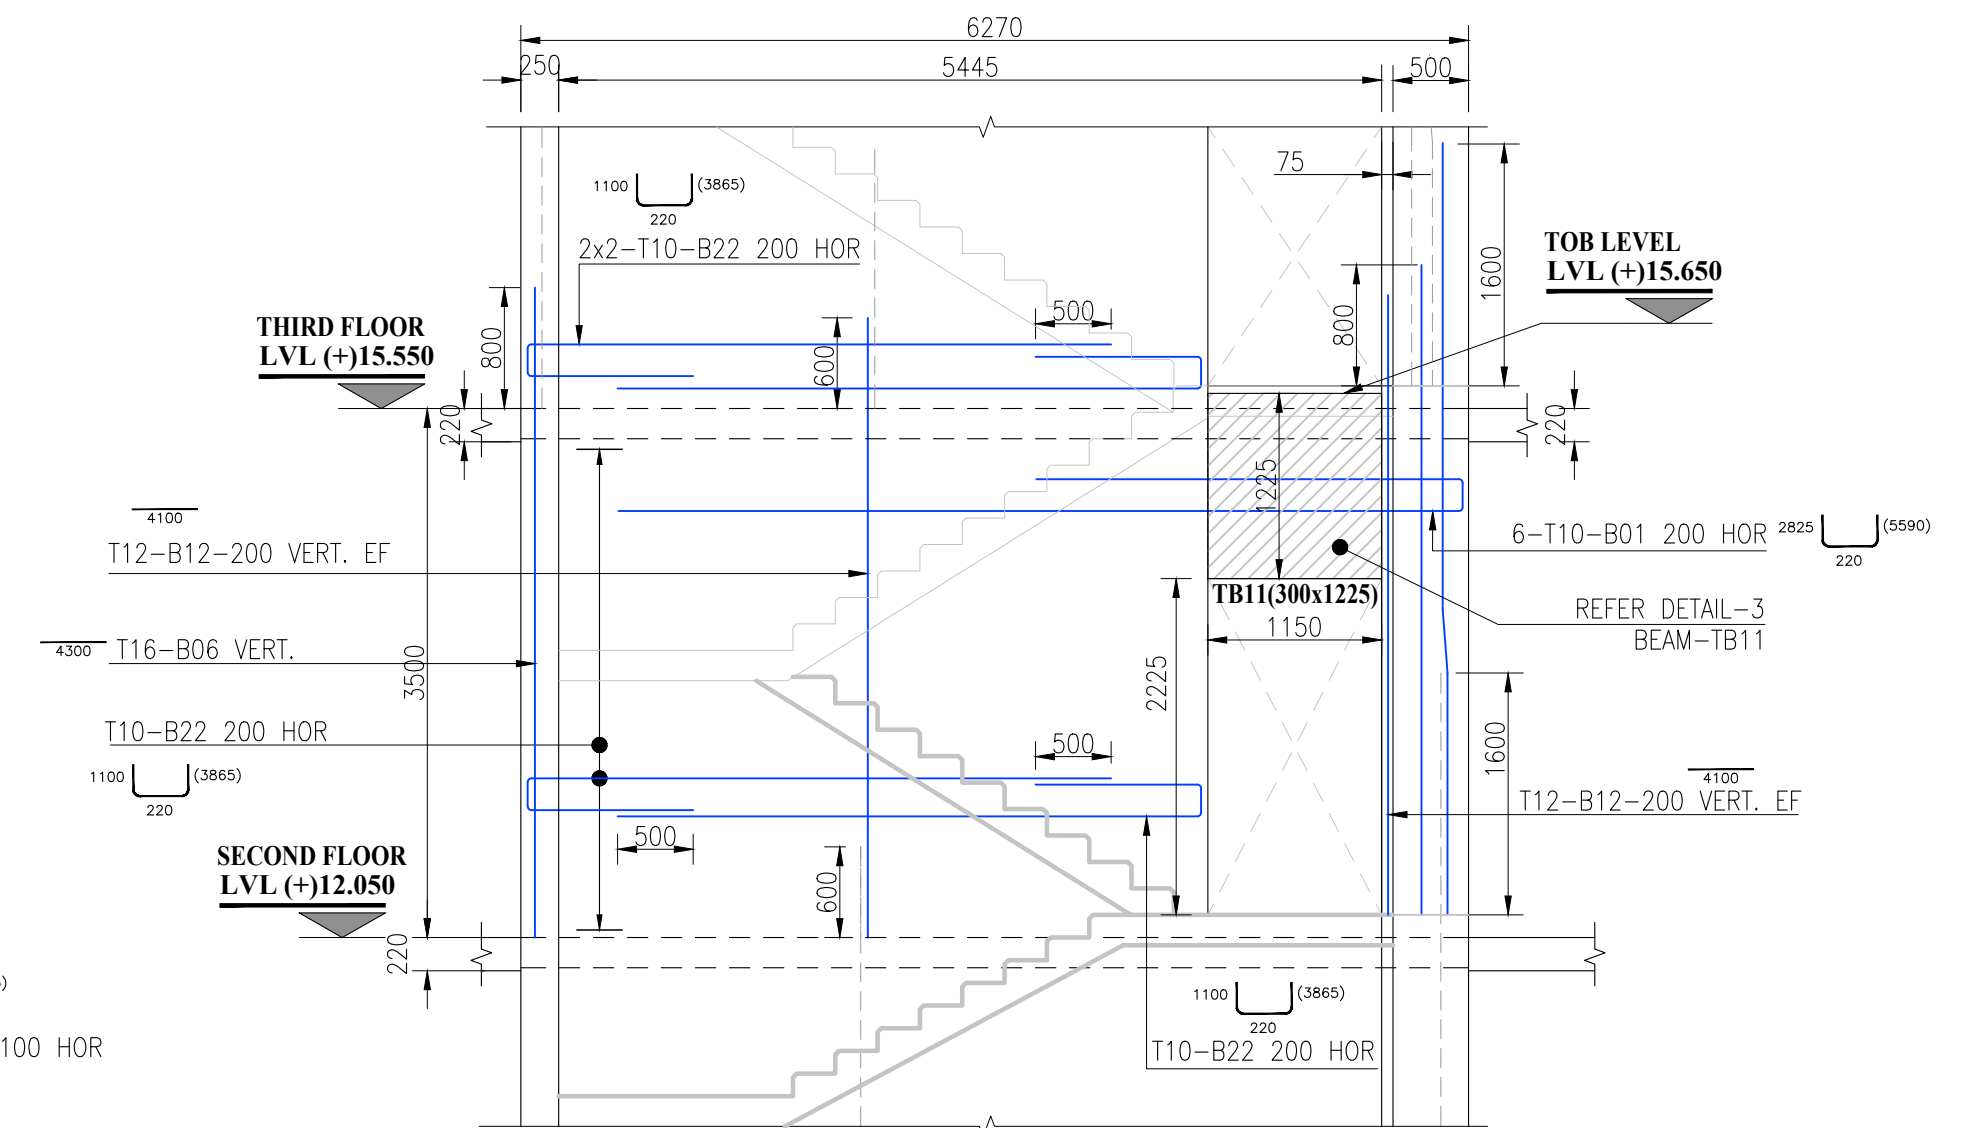


ELEVATION-B
SCALE: 1:50

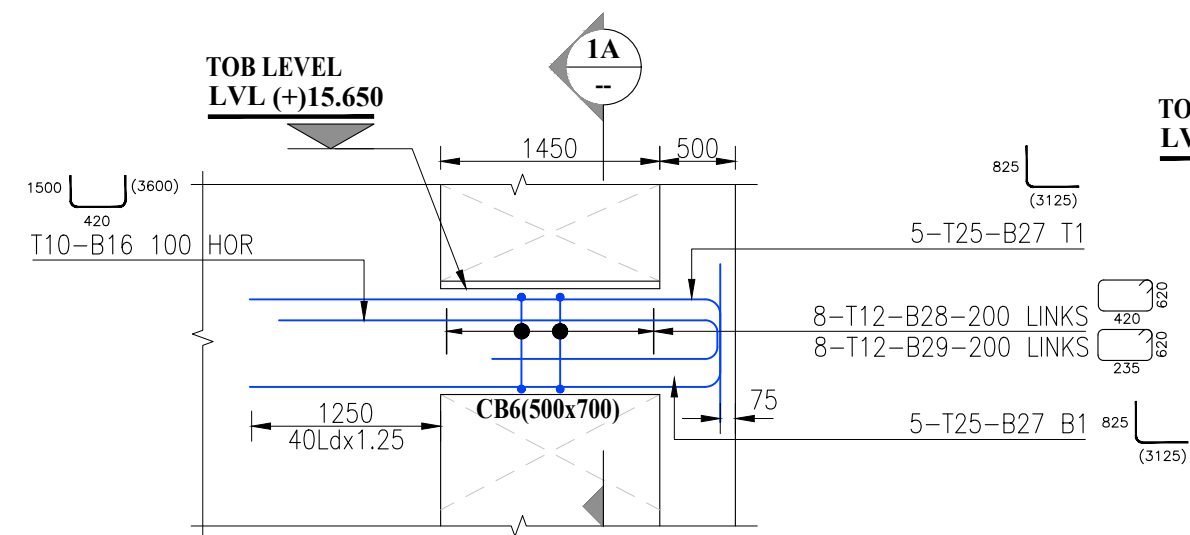


DETAIL-1
SCALE: 1:50

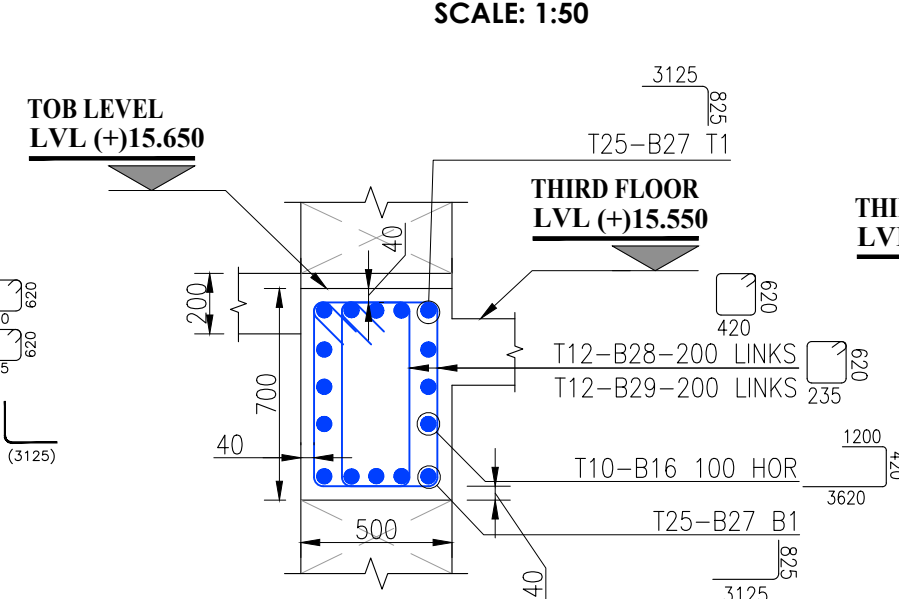


SECTION-1A
SCALE: 1:25

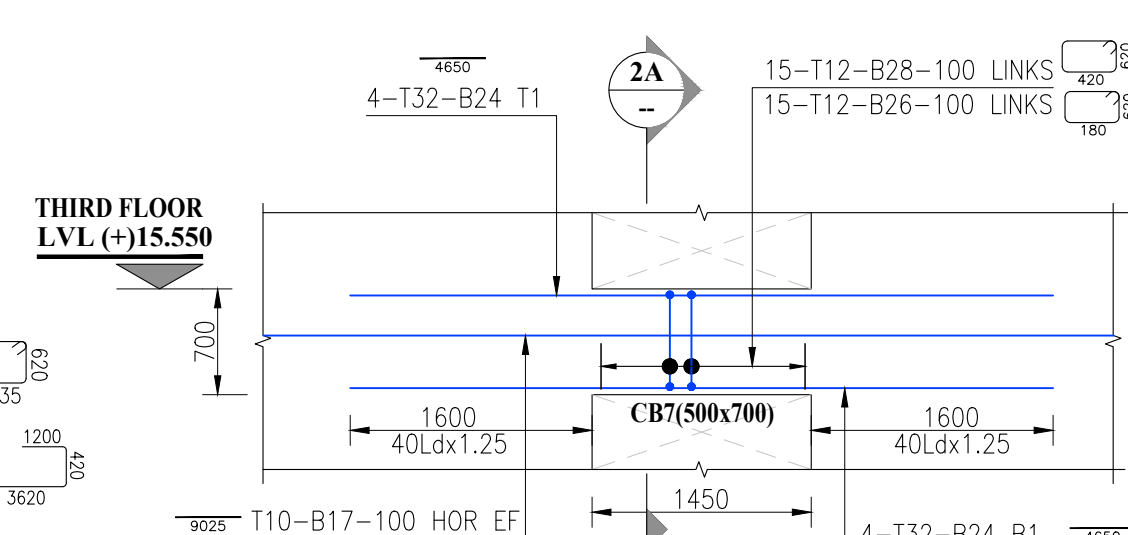


DETAIL-2
SCALE: 1:50

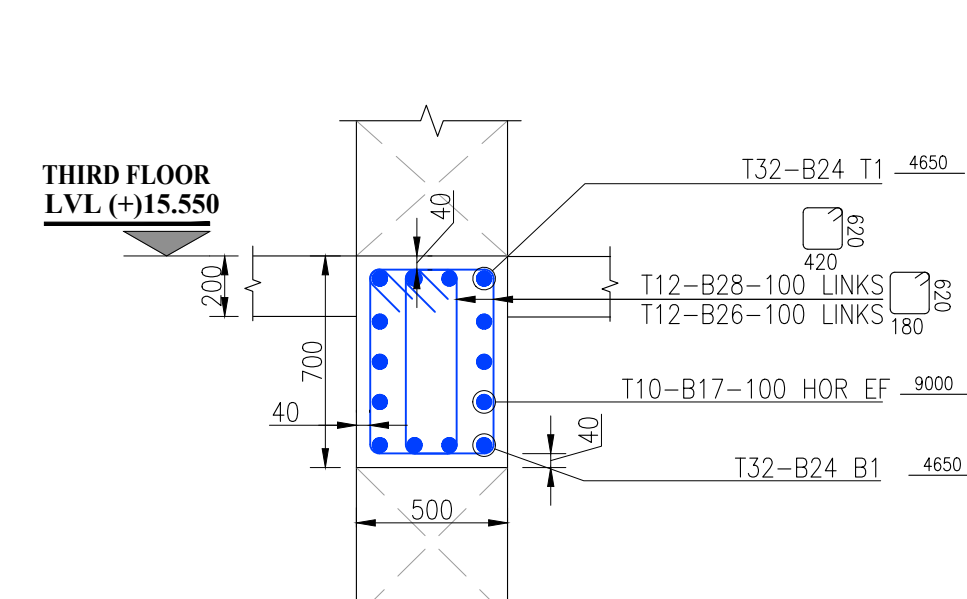


SECTION-2A
SCALE: 1:25

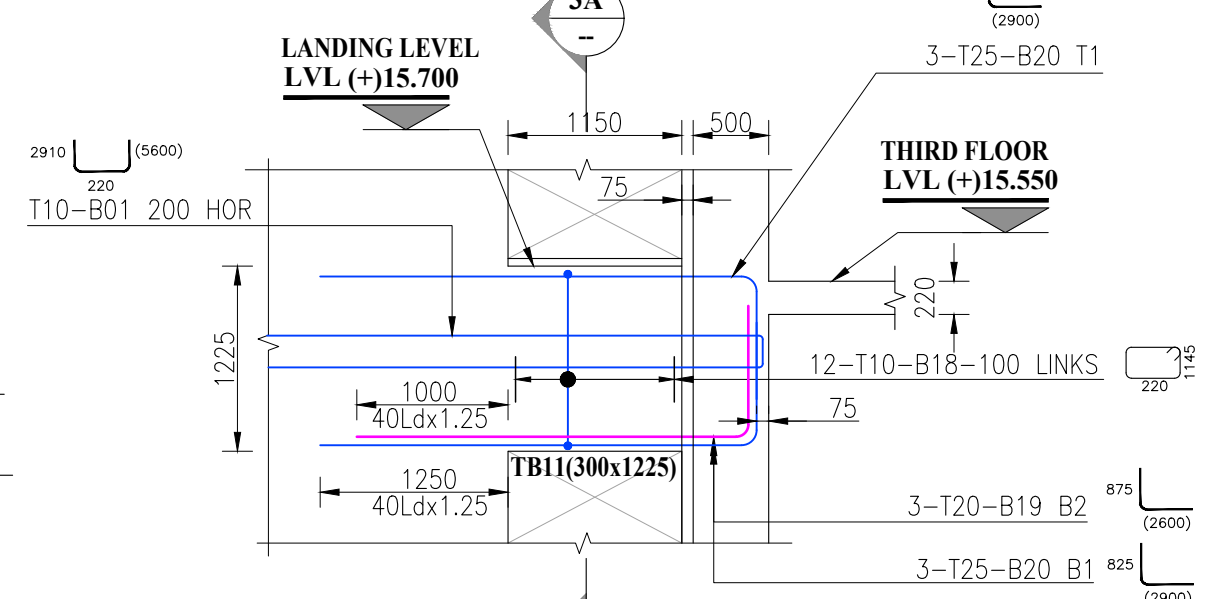


DETAIL-3
SCALE: 1:50

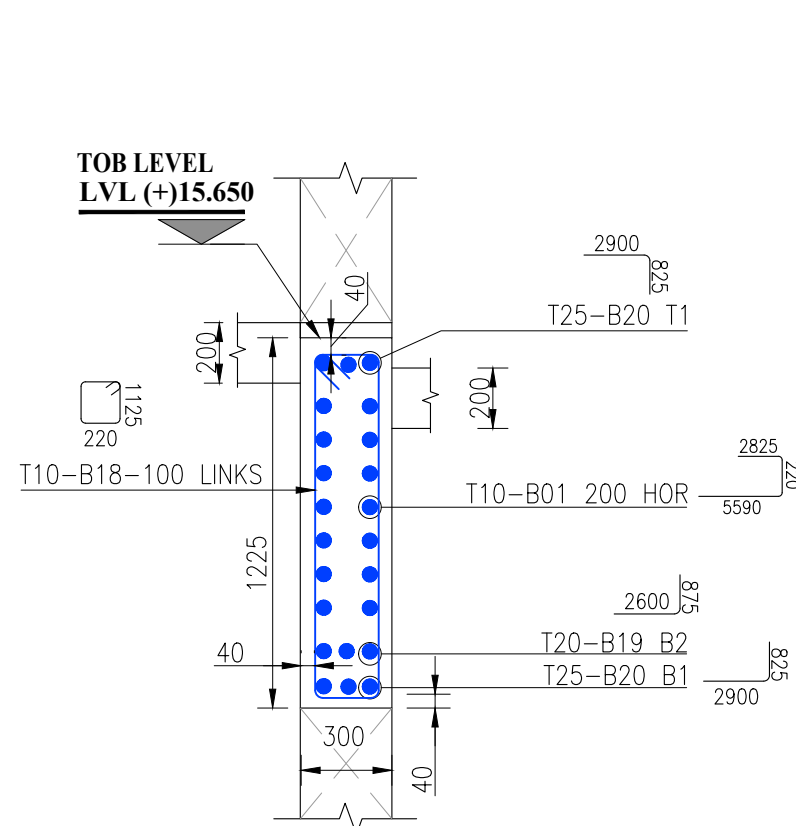


SECTION-3A
SCALE: 1:25

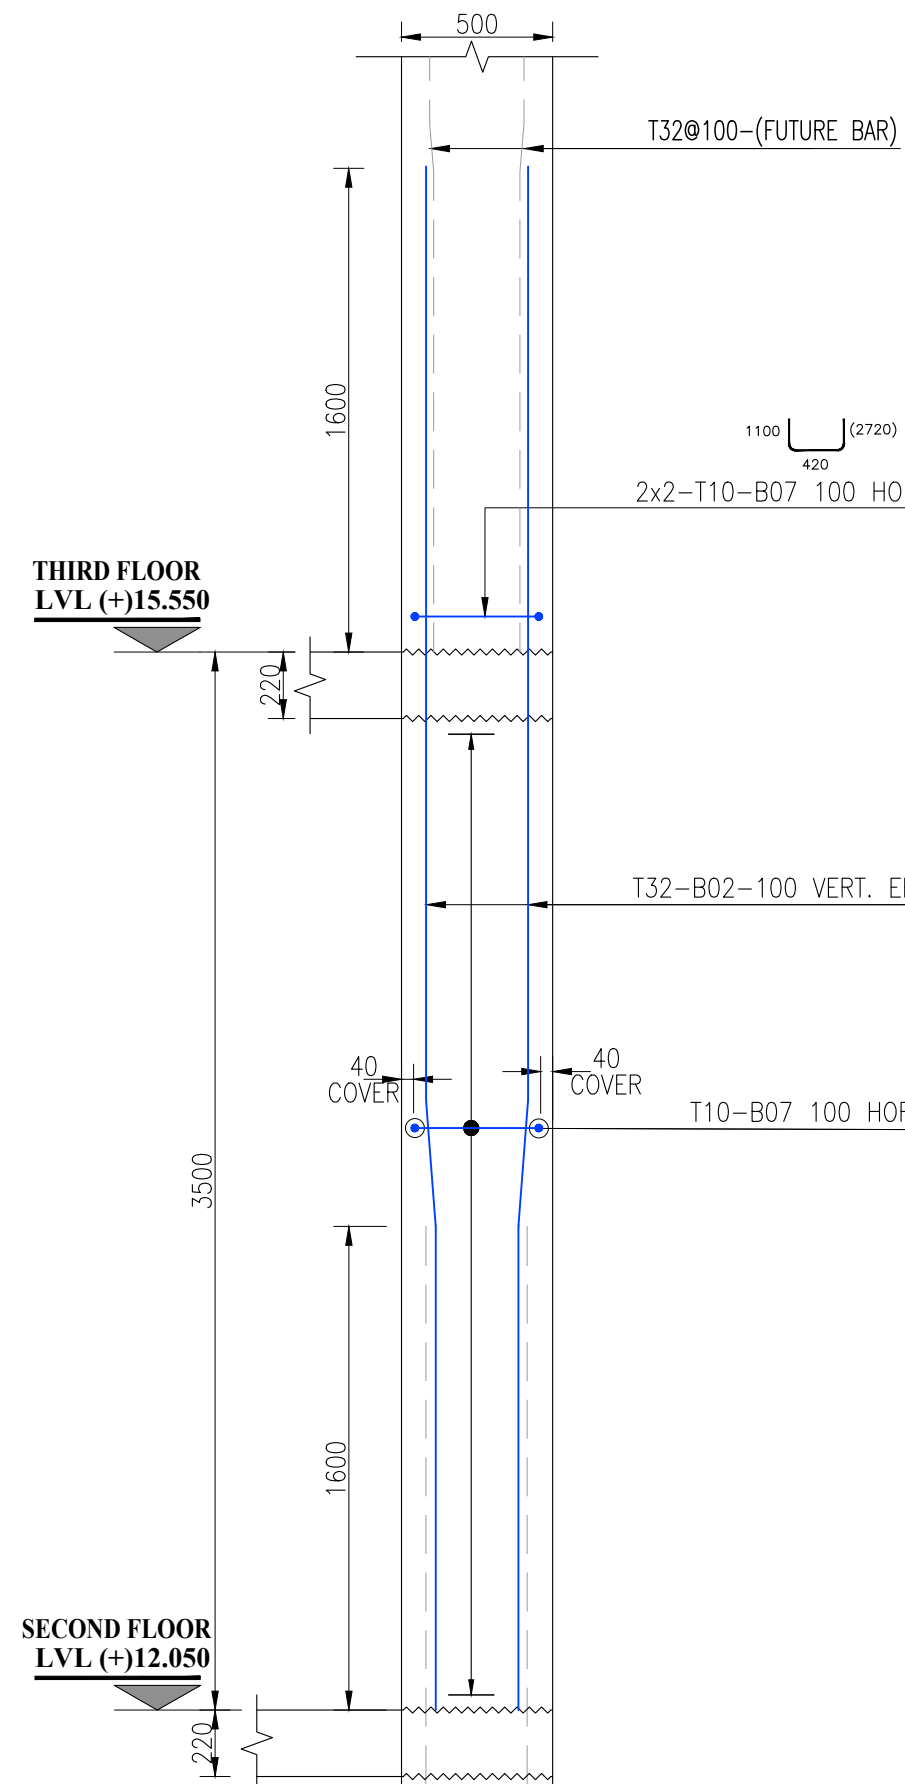


SECTION-1
SCALE: 1:25

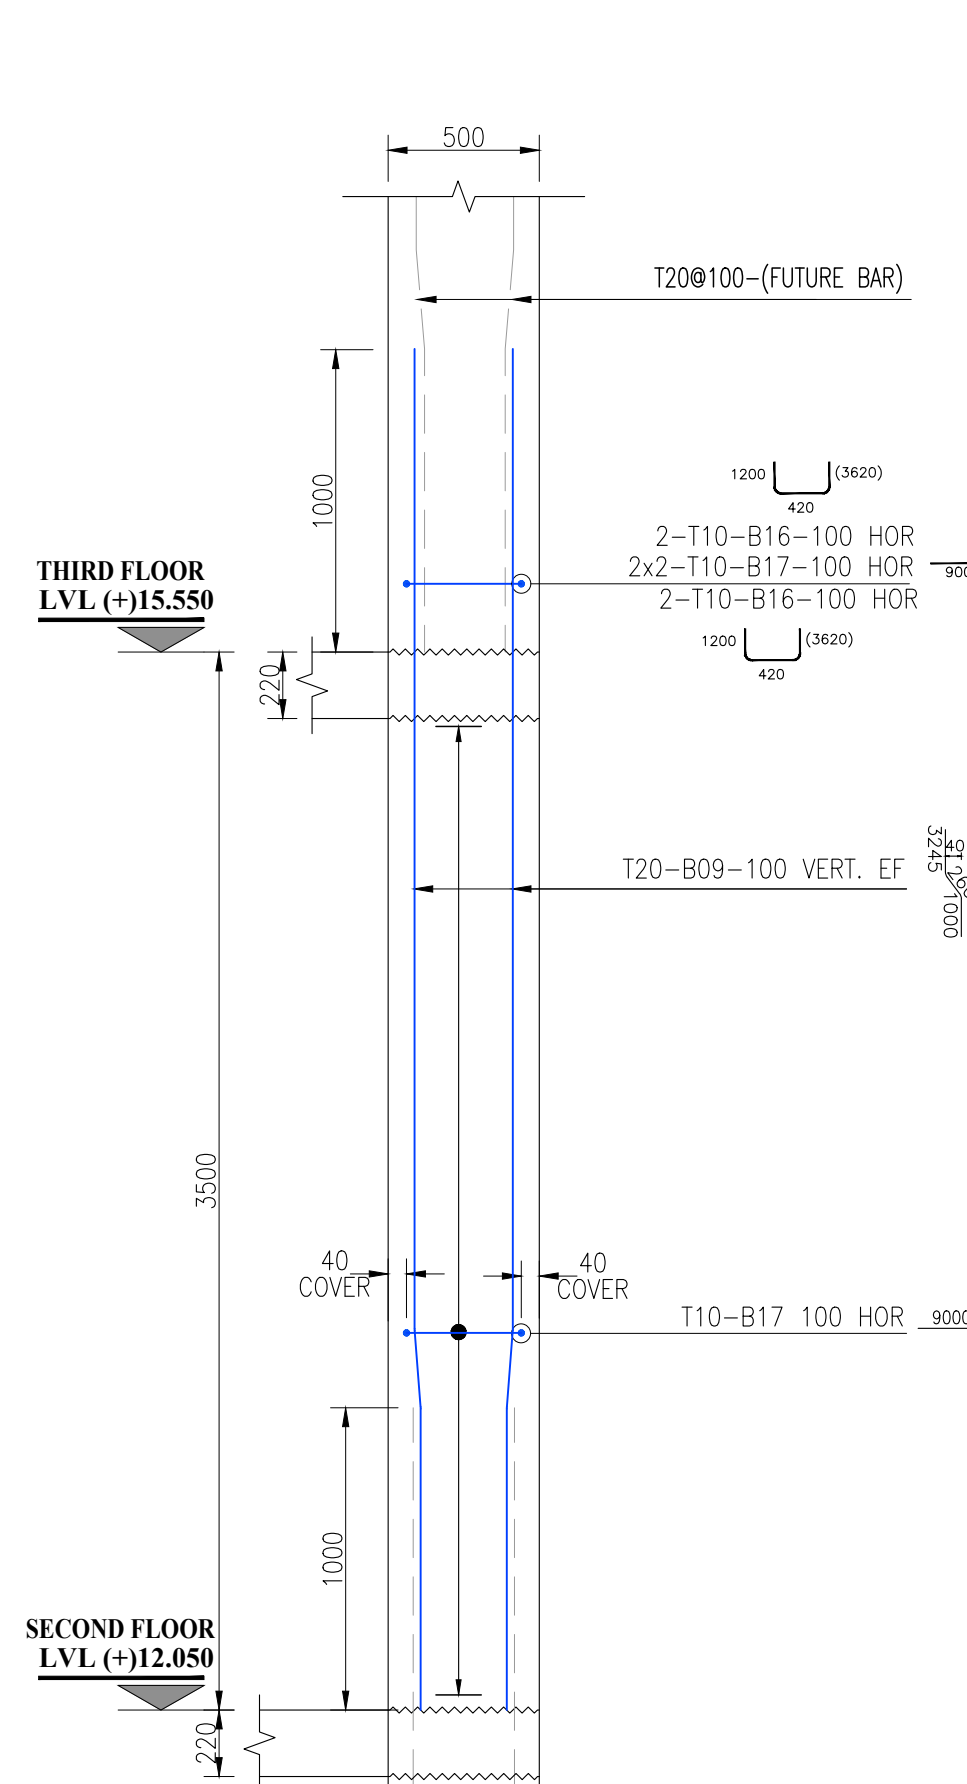

SECTION-2
SCALE: 1:25

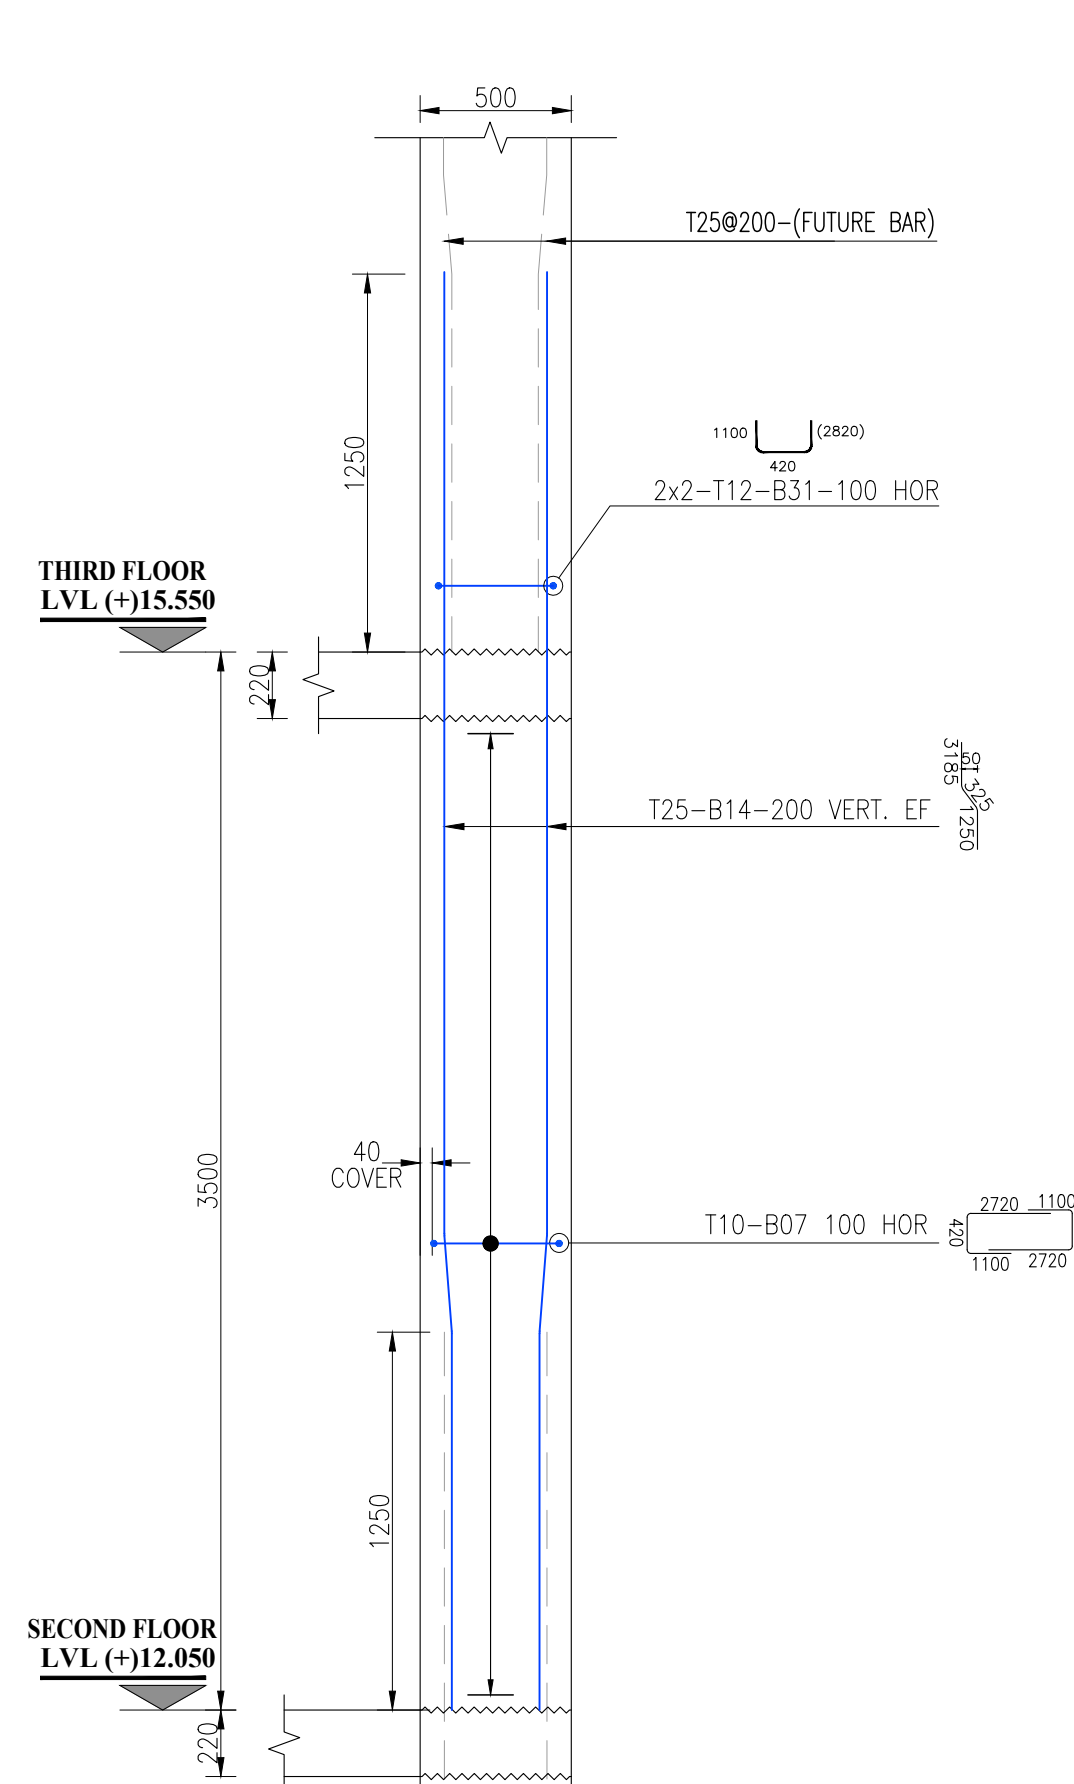

SECTION-3
SCALE: 1:25

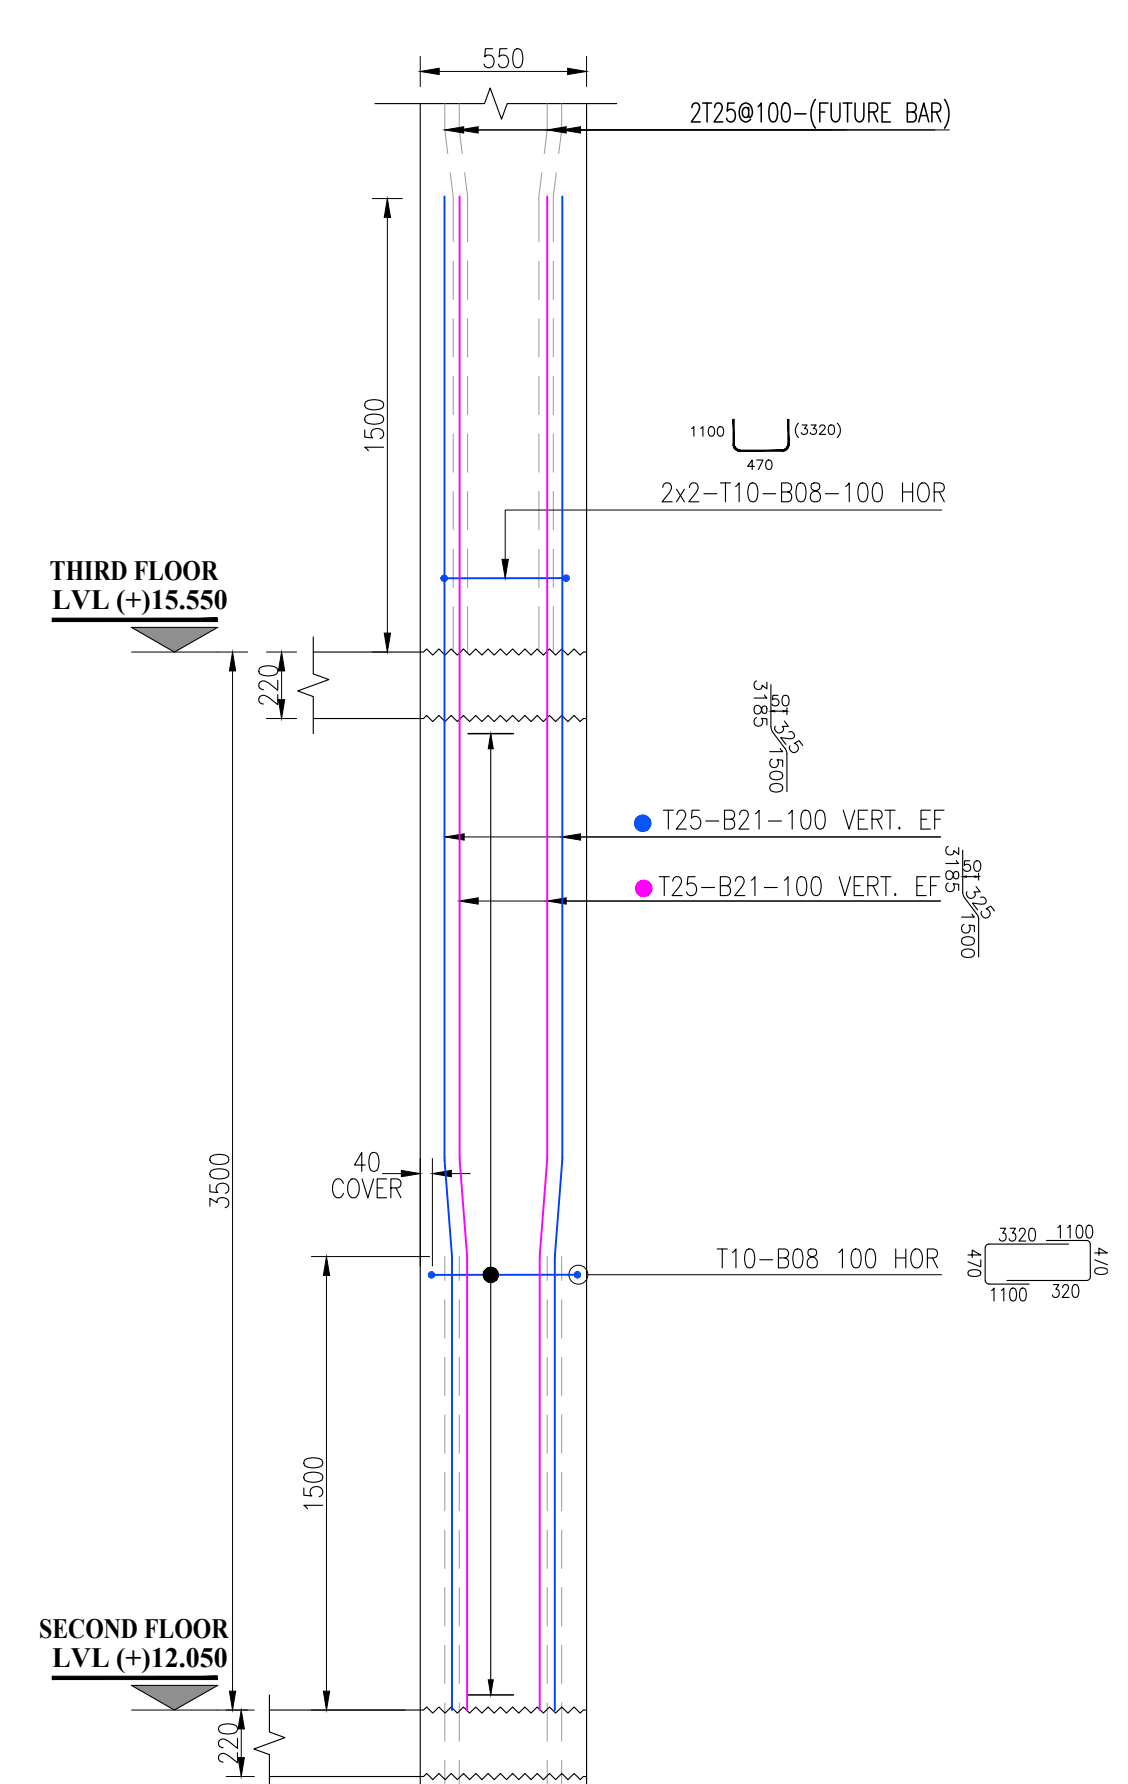

SECTION-4
SCALE: 1:25