


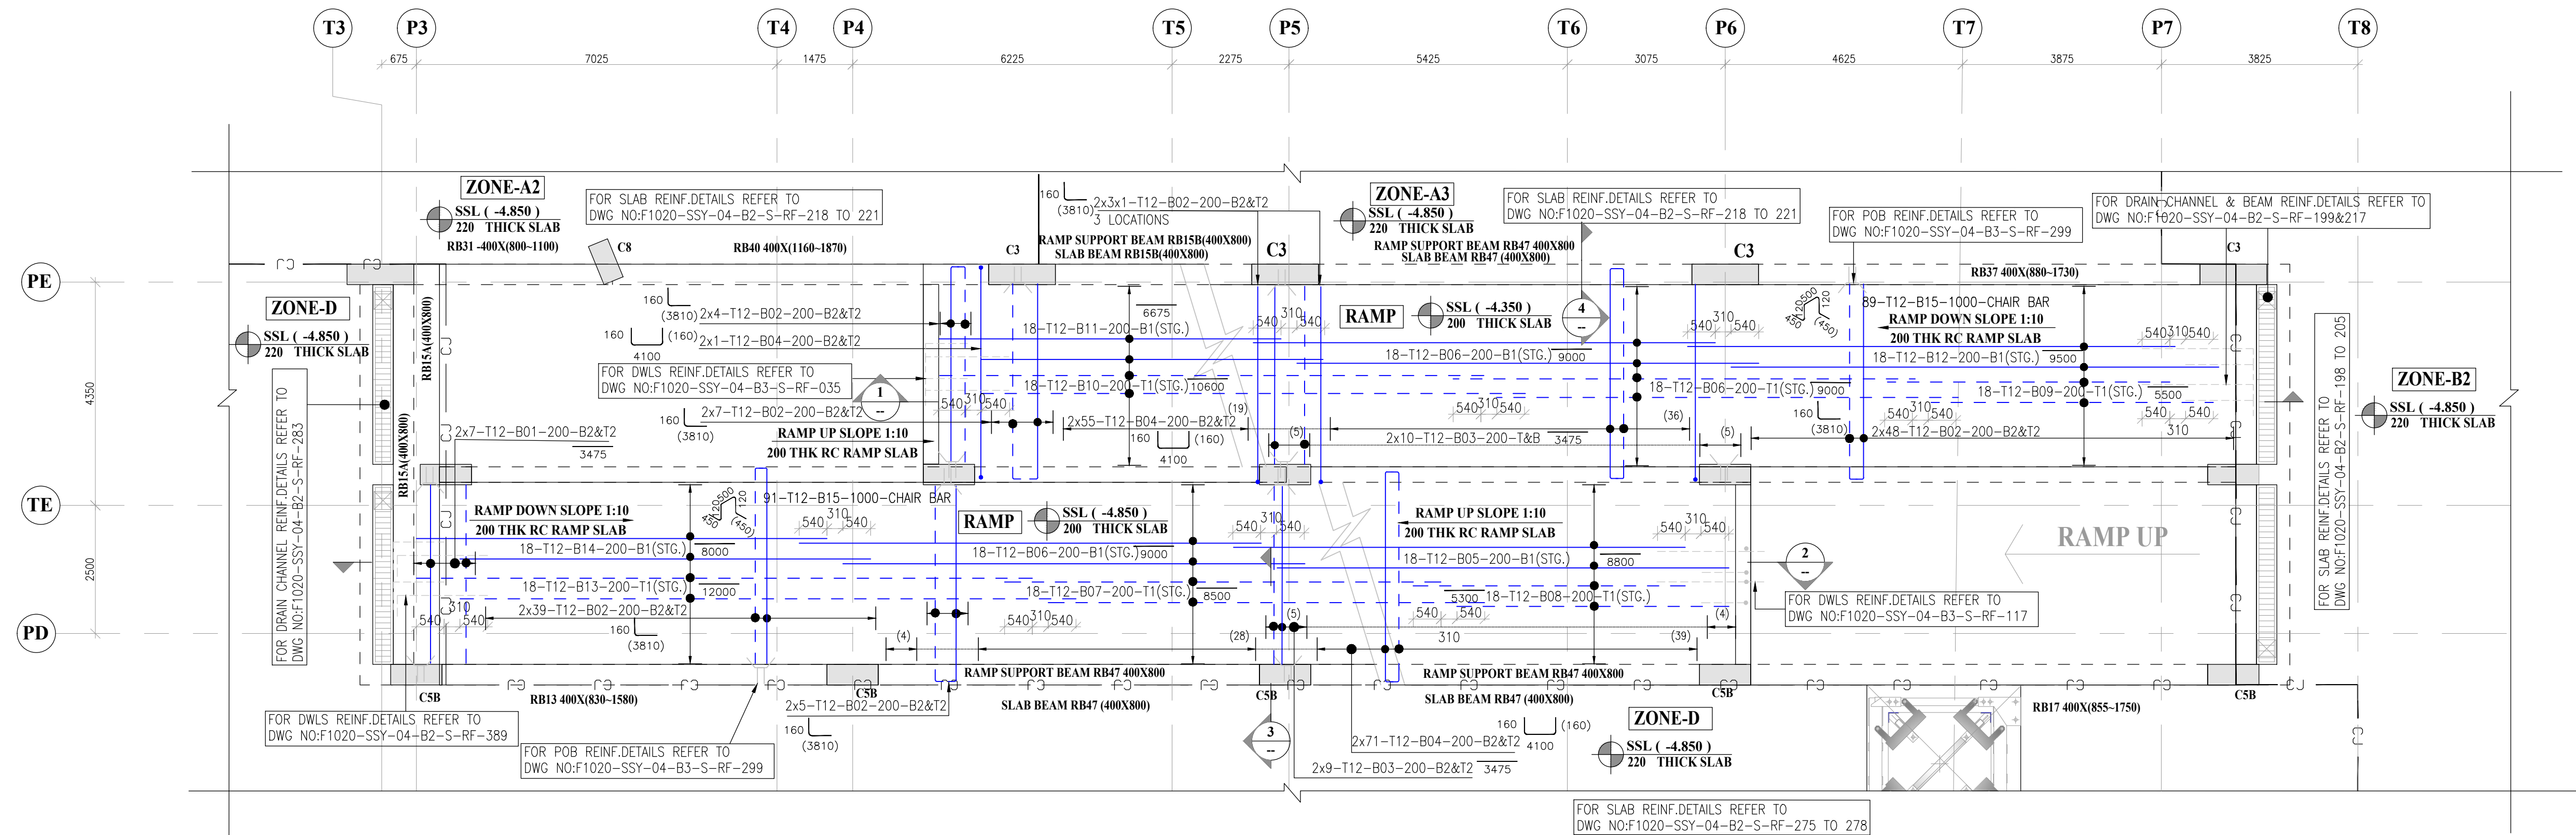

PLOT-4 BASEMENT-03 TO BASEMENT 02 RAMP NFORCEMENT DETAILS

