




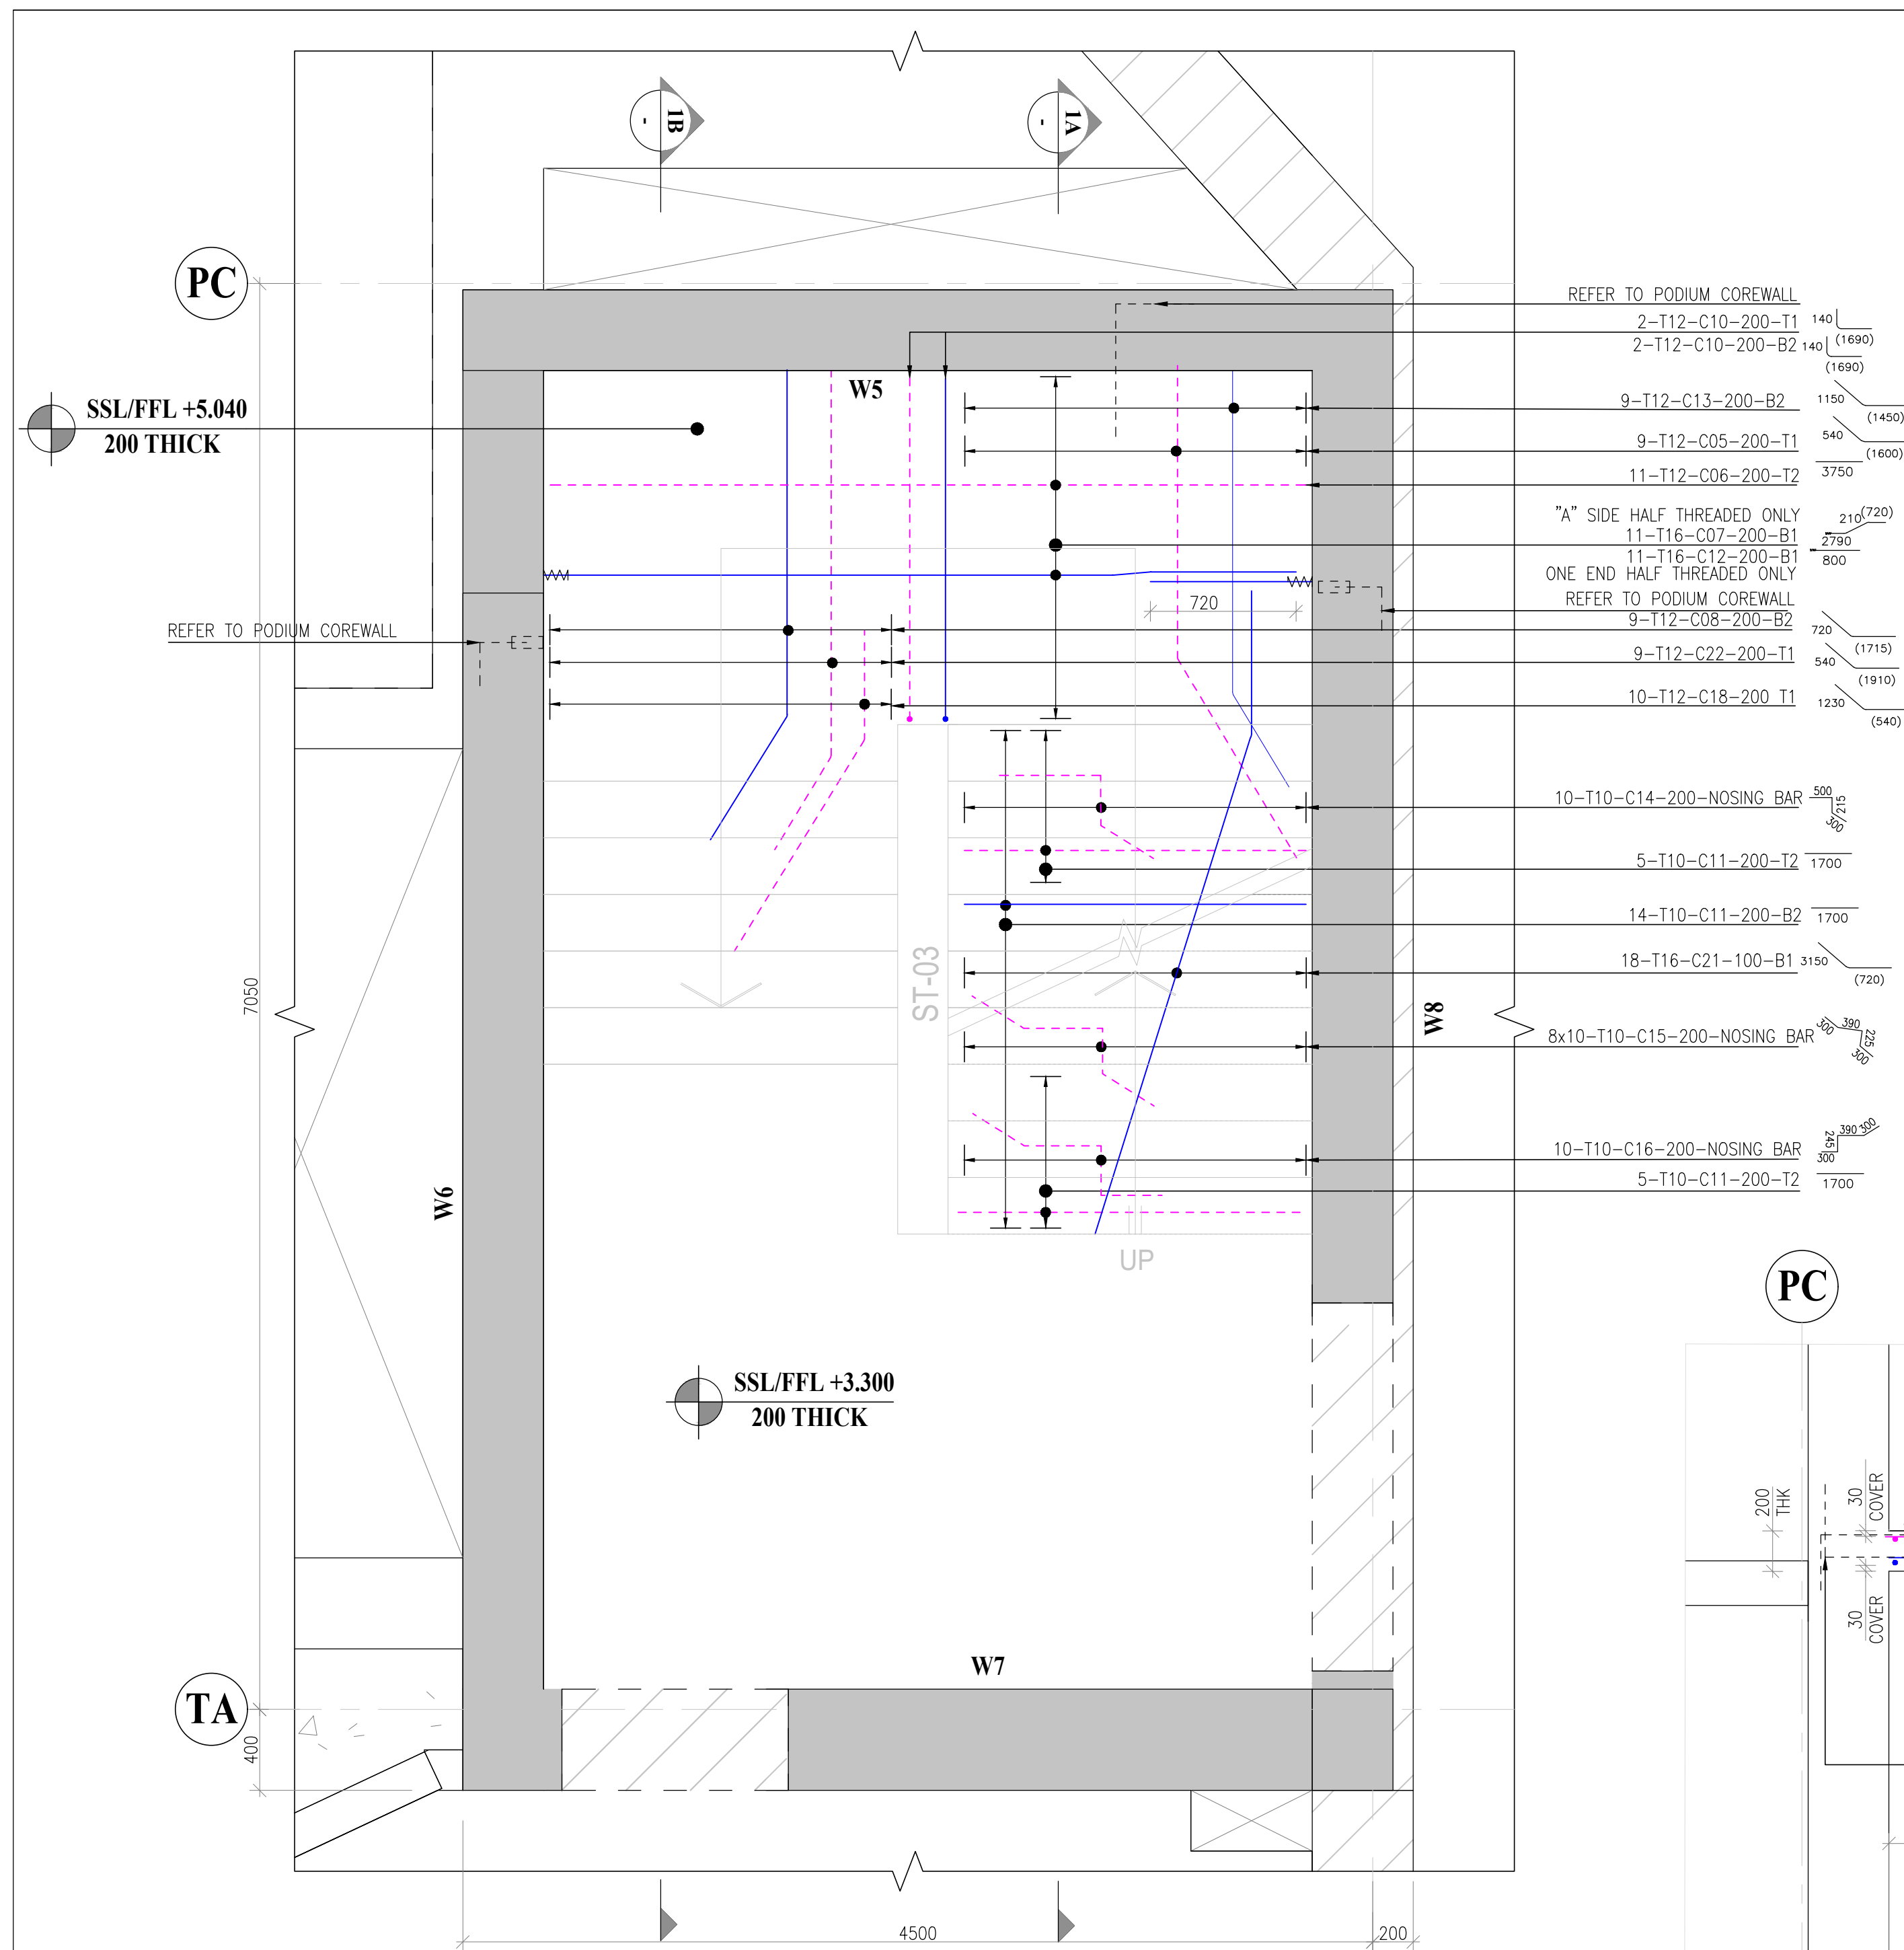


**PLOT-4 STAIR CASE 03 REINFORCEMENT DETAILS
FROM +3.300 TO +5.040 LEVEL**
GRIDS BET. (TA-PC)-(P12)
SCALE: 1:25

P12

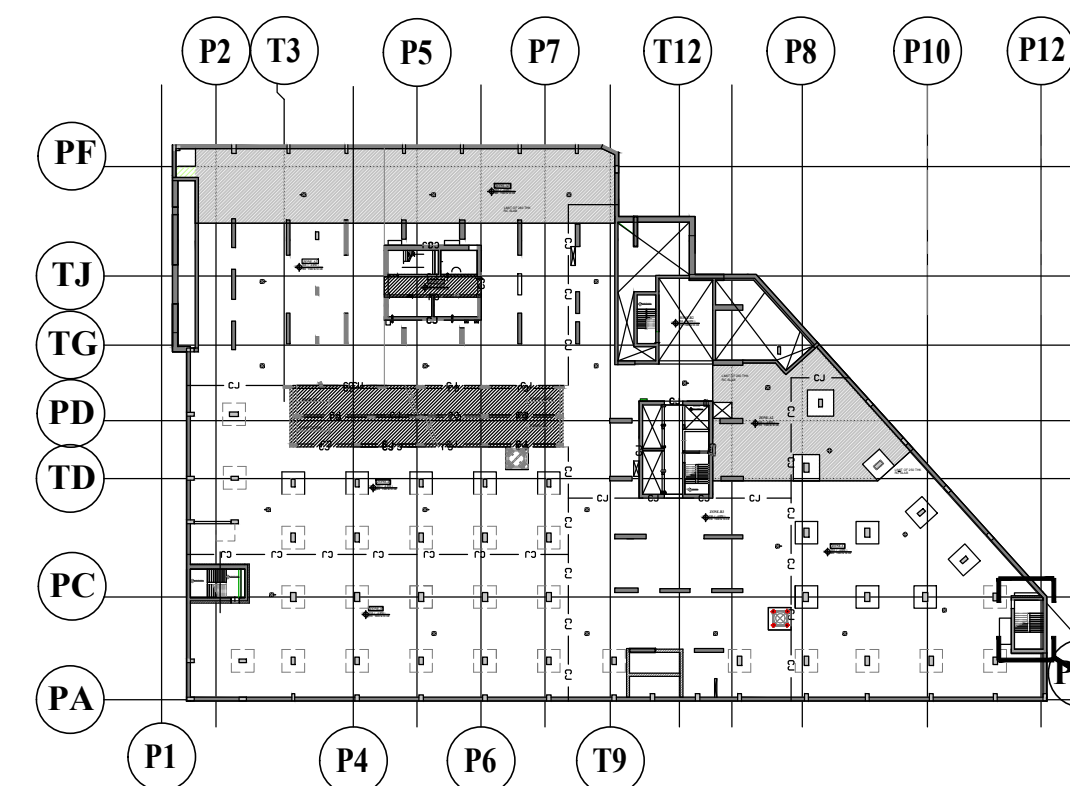

KEY PLAN

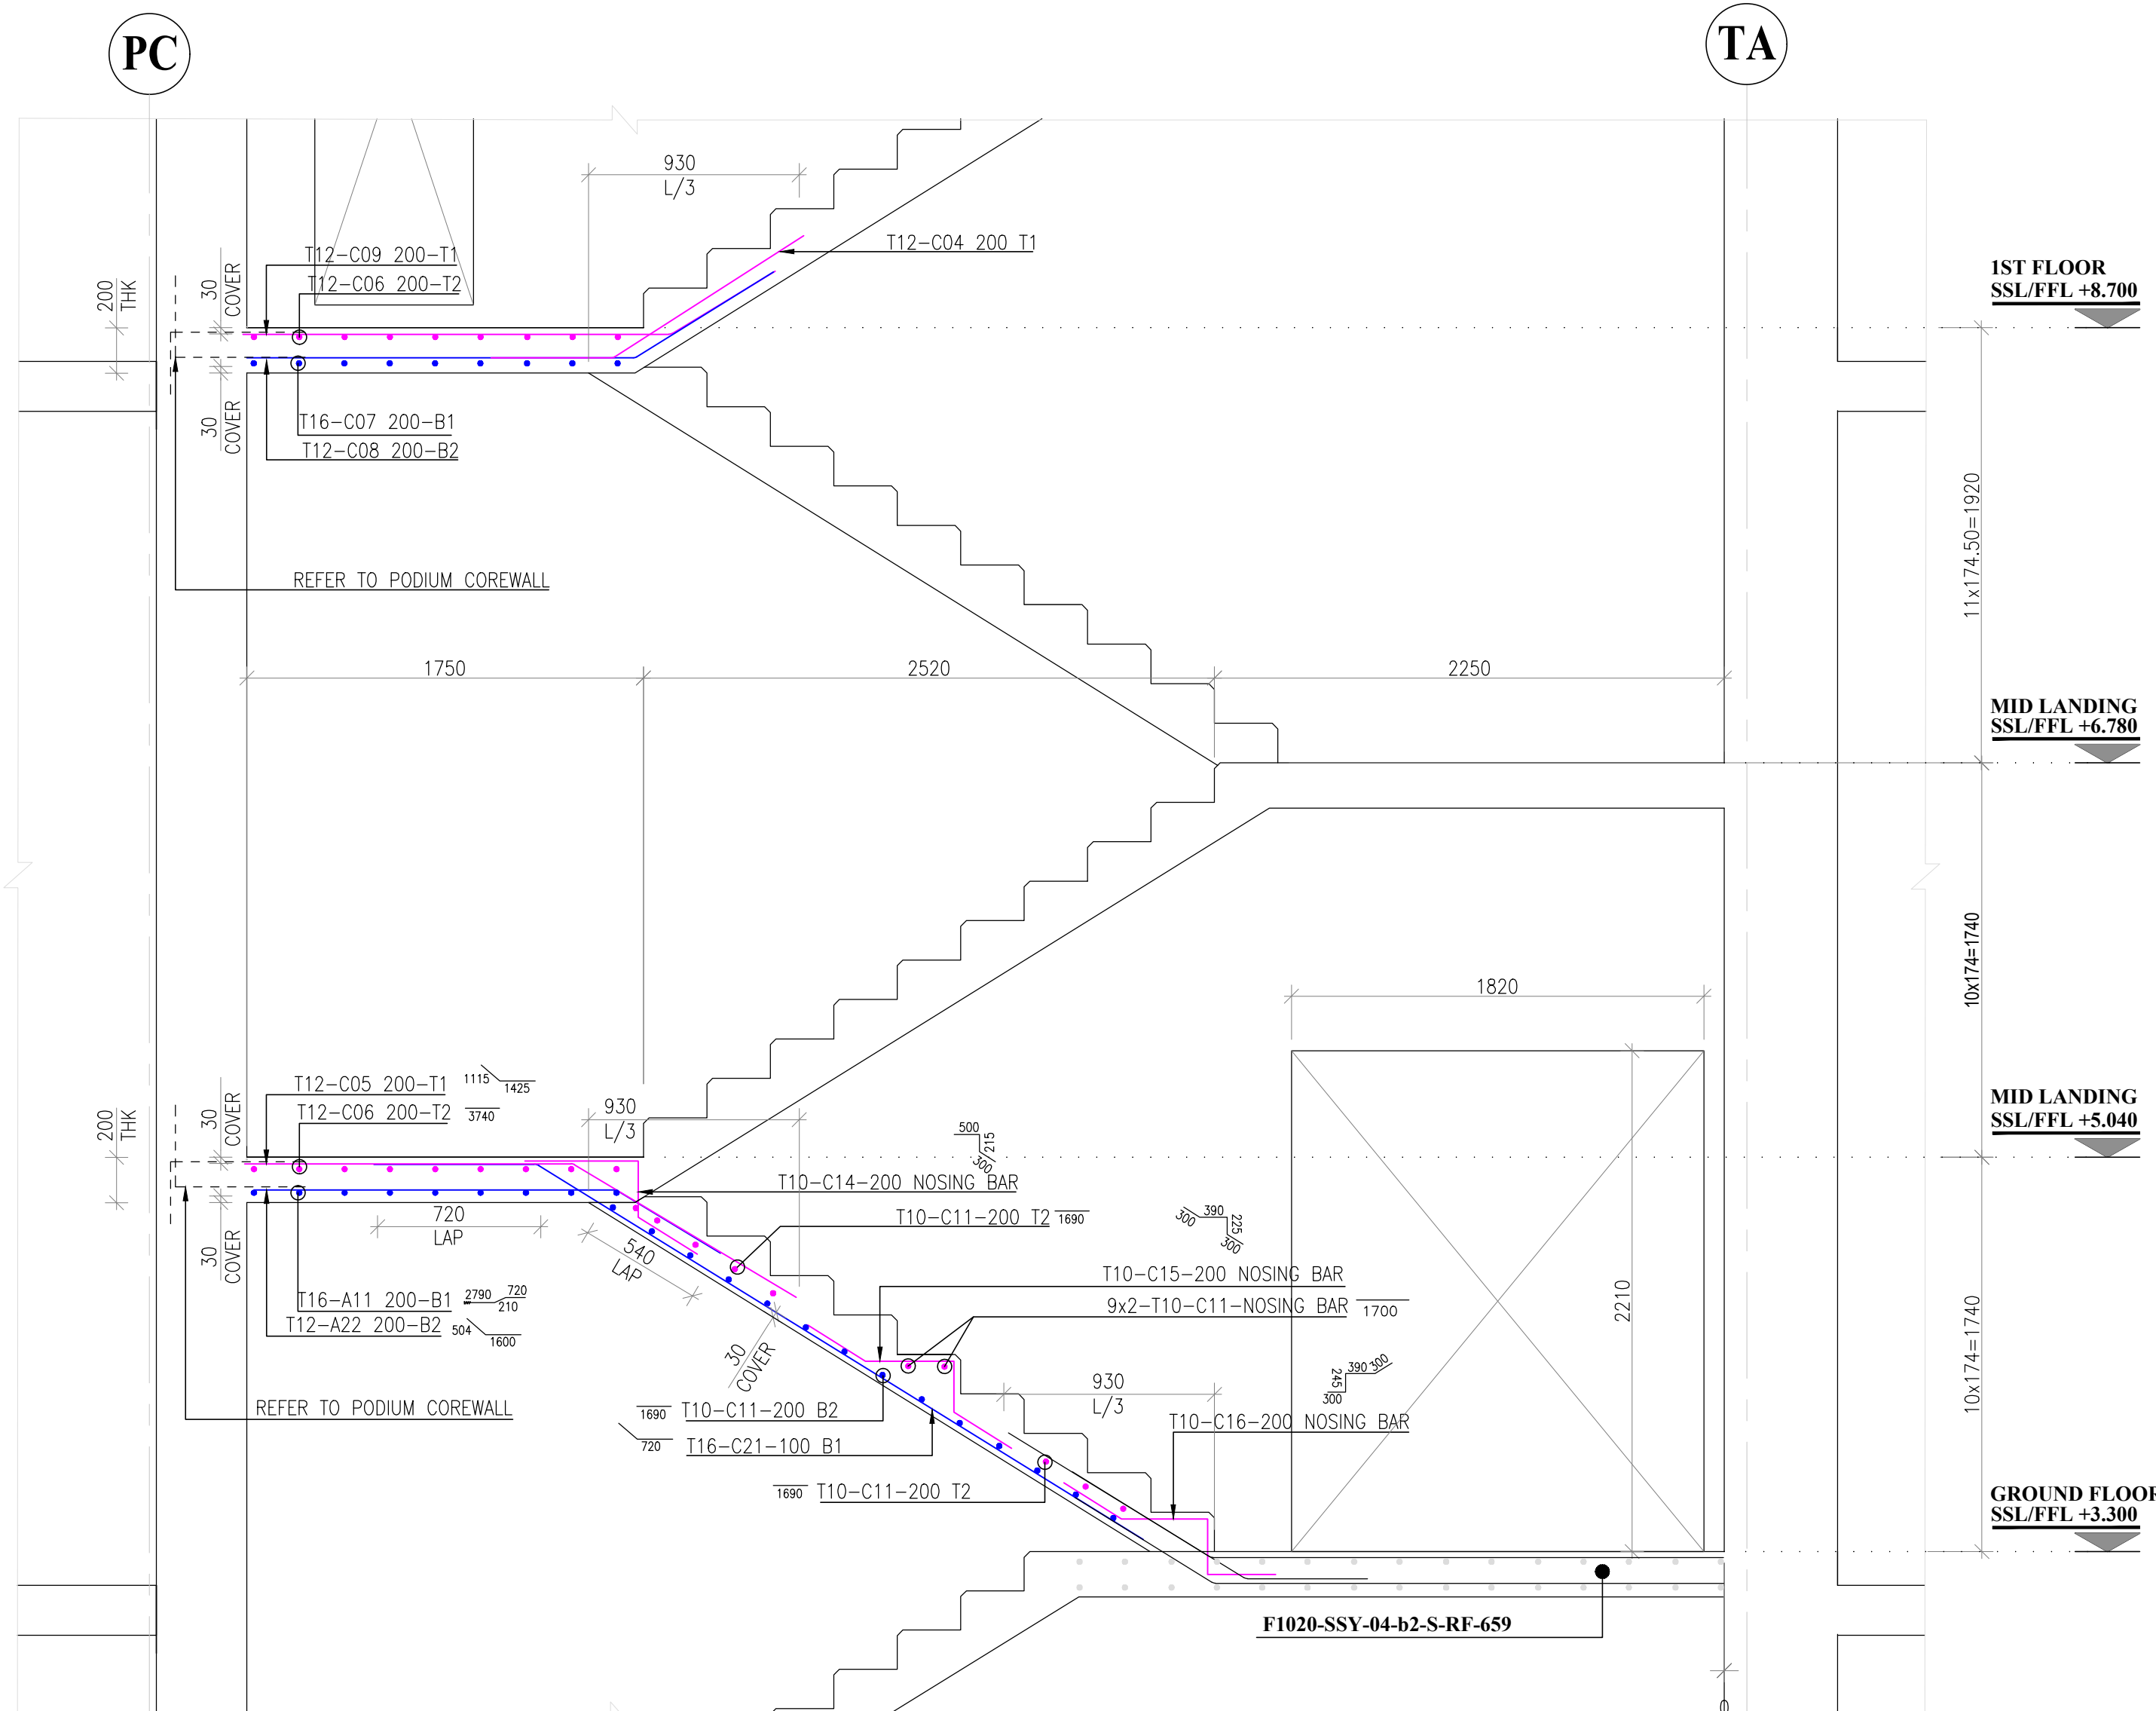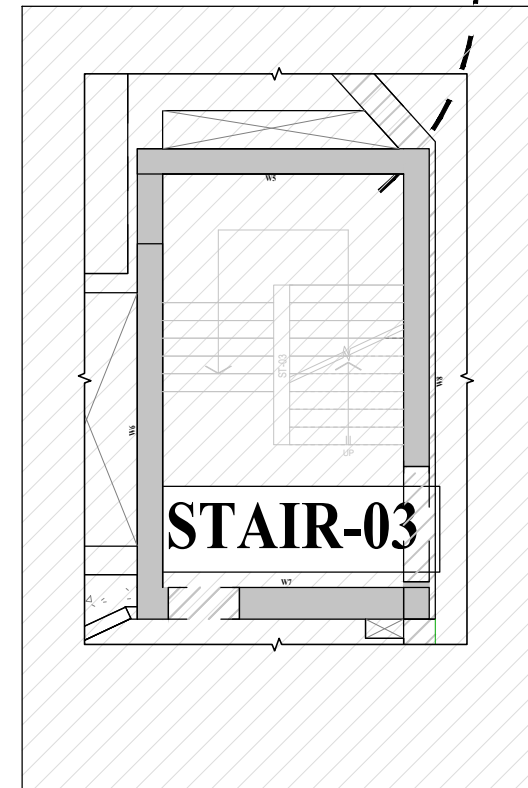

SECTION 1A-1A
SCALE: 1:25