

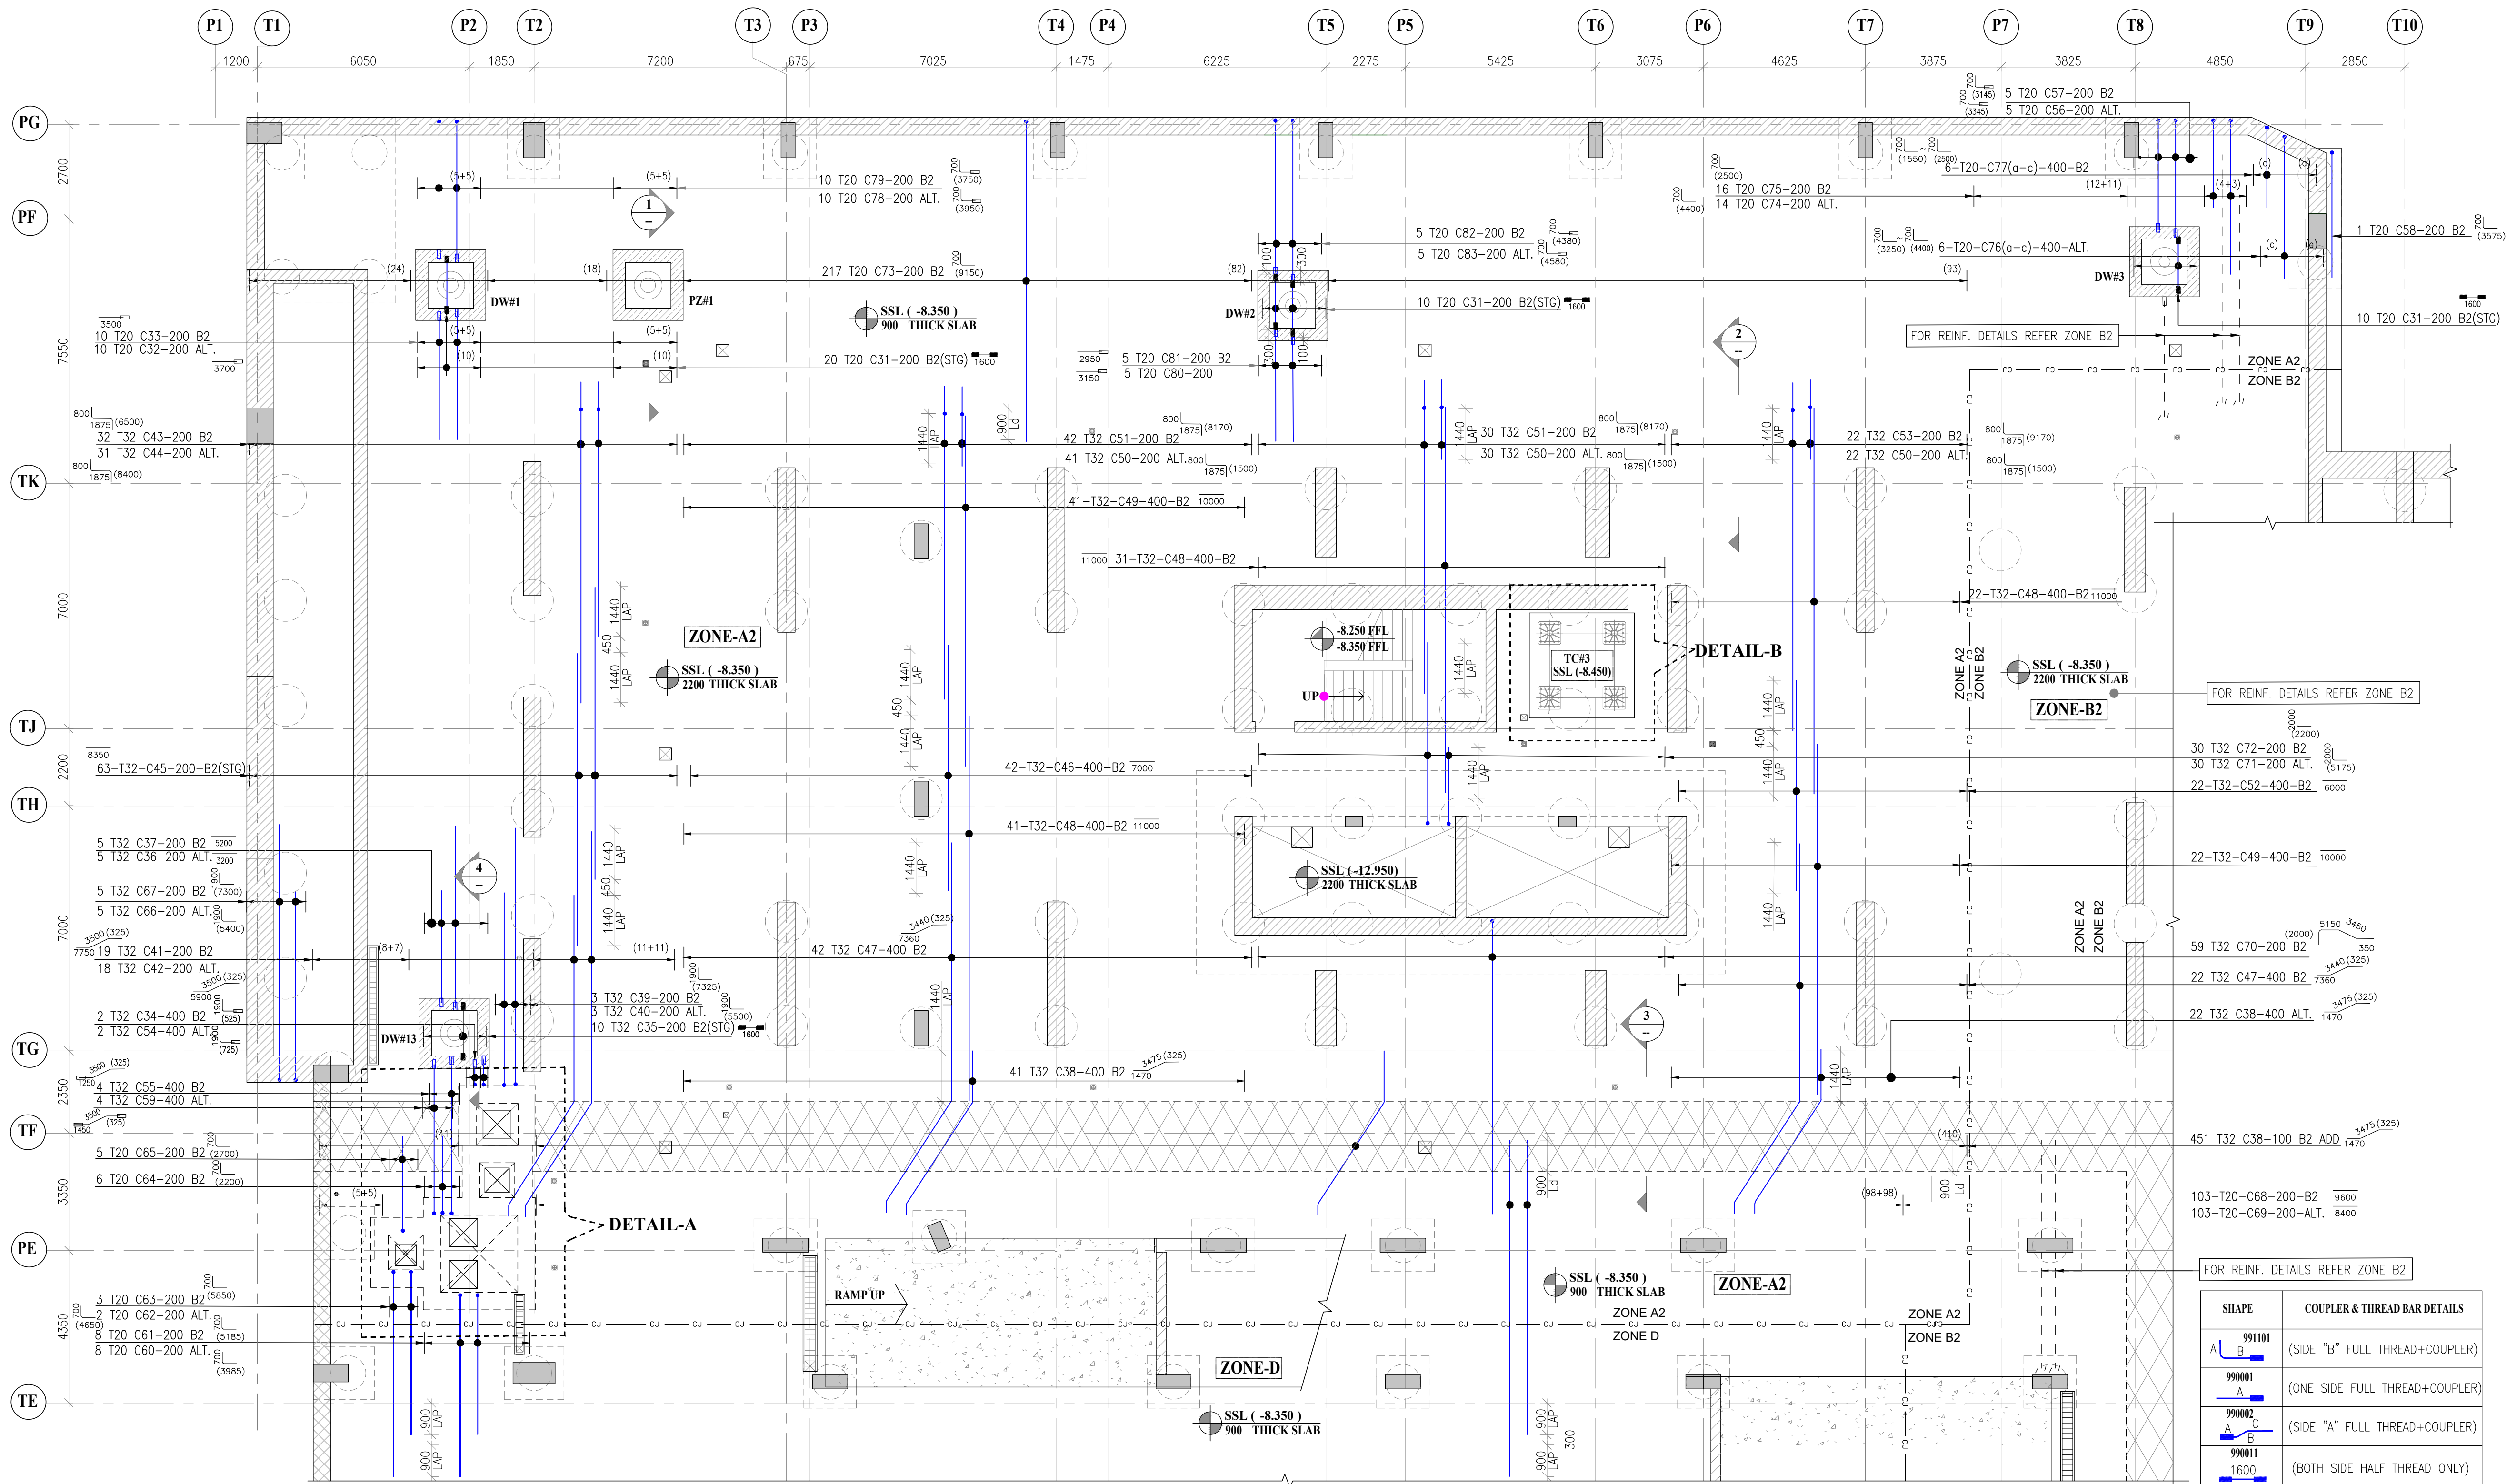


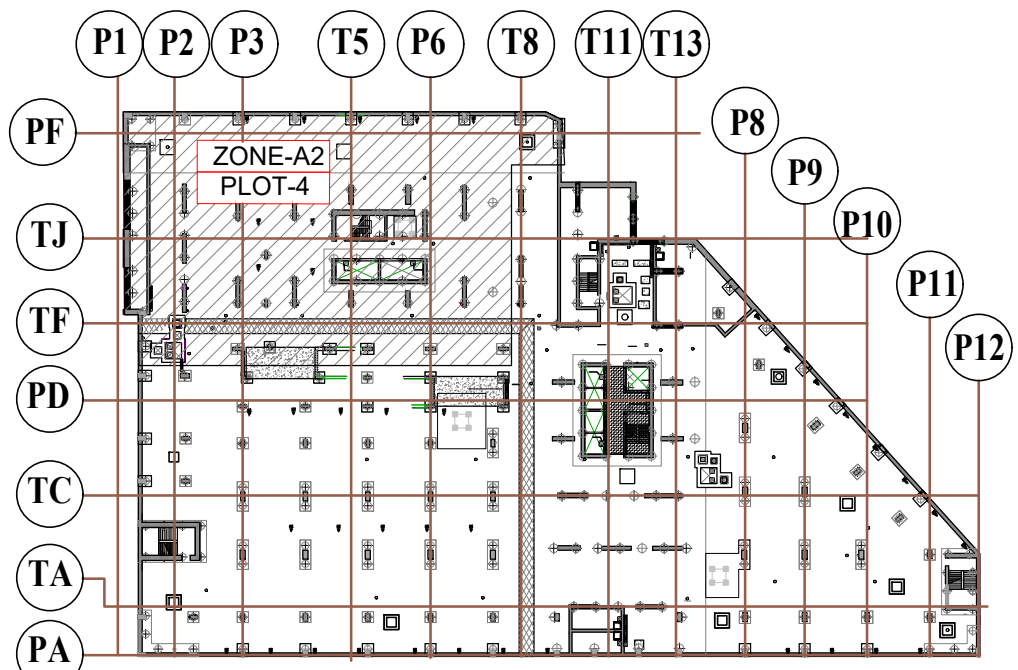

\*FOR RAFT REINFORCEMENT  
1.FOR RAFT B1&T1,T2 LAYER REINF.DETAILS REFER TO DWG NO:F1020-SSY-04-B3-S-RF-035&39,40  
2.FOR RAFT ADD'L X&Y DIR. LAYER REINF. DETAILS REFER TO DWG NO:F1020-SSY-04-B3-S-RF-040 TO 043

**PLOT-4 BASEMENT 03 (ZONE A2) RAFT SLAB  
BOTTOM (B2 LAYER) REINFORCEMENT DETAILS**

SCALE 1:100

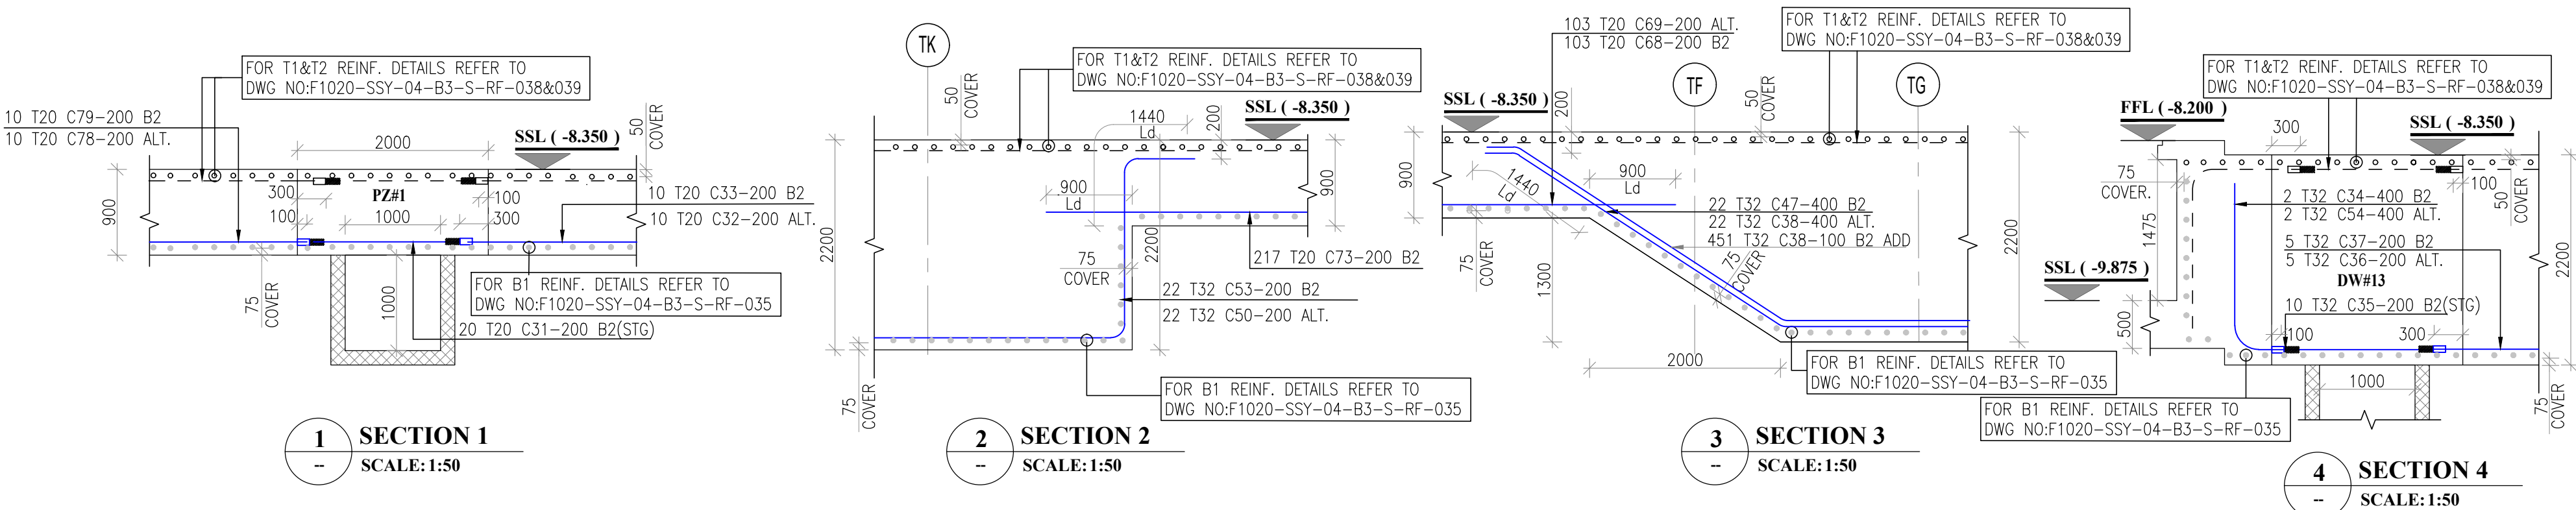

**KEY PLAN  
SCALE NTS**